
The Burrow / life above and below

World section at X=-30 m / homes and public streets continue beneath the outdoor settlement

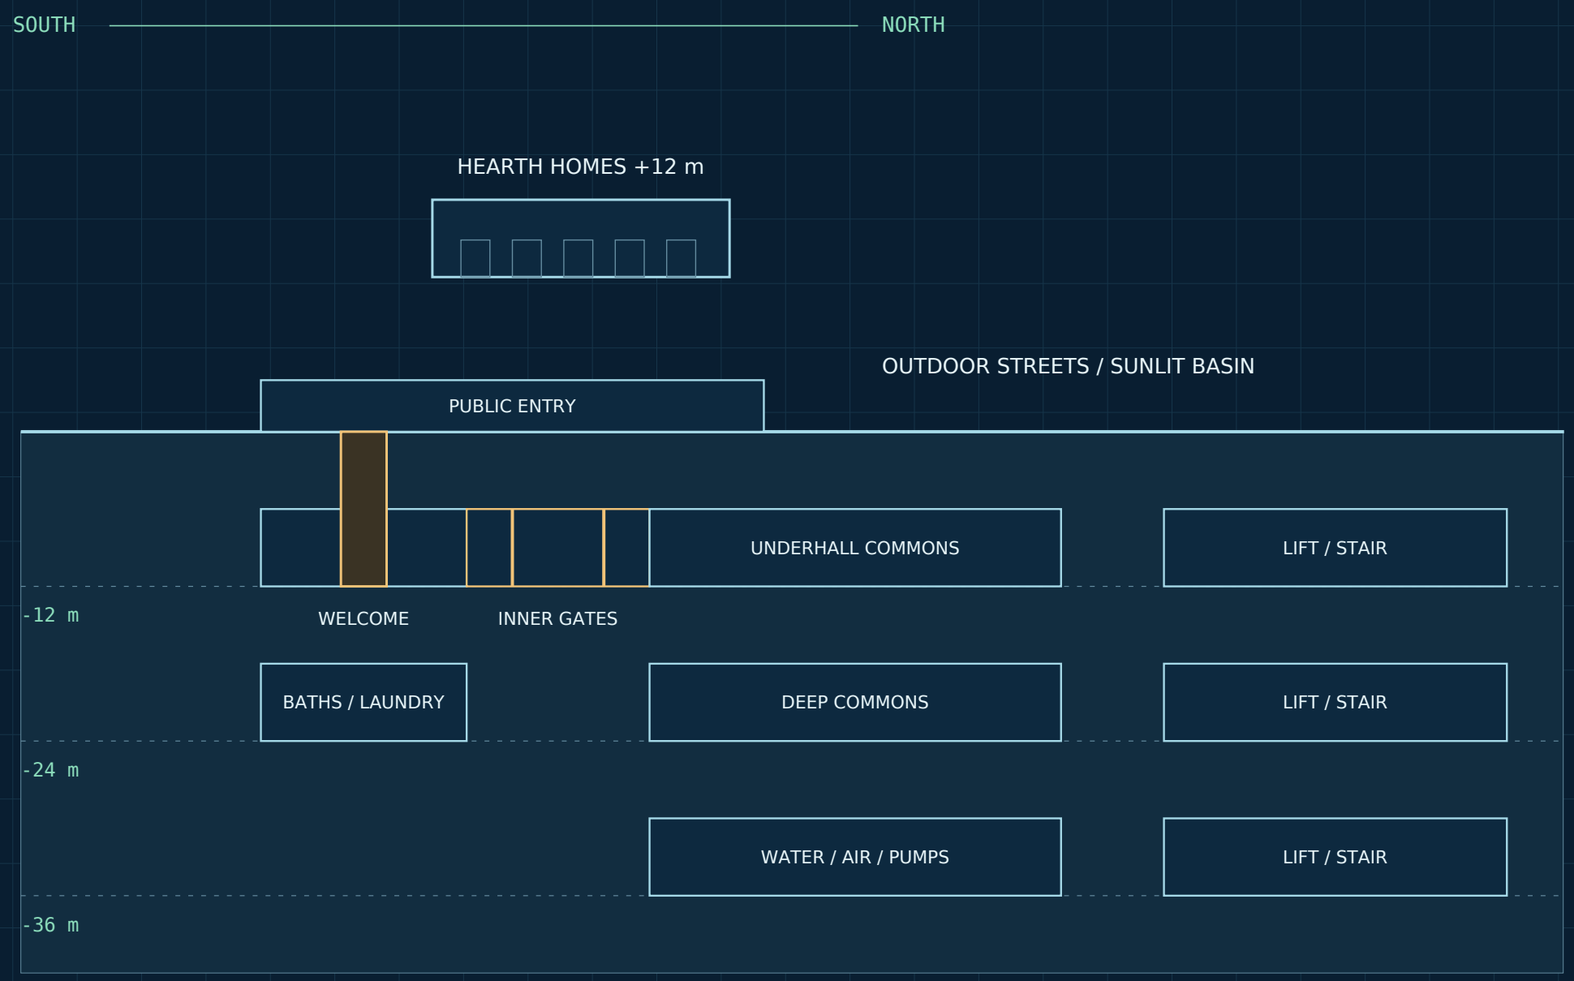

Section uses vertical exaggeration for clarity. Primary floor levels and Y positions are fixed.

Residential wards flank the commons east and west; they sit outside this section cut.

Above: busy markets, gardens and homes. Below: two populated neighborhood levels, then maintainable services. The refuge is a part of normal civic life, ready to receive surface residents if needed.

ONE SHARED TOWN

The outdoor Burrow remains important. Underground streets are also permanent, crowded neighborhoods with their own daily rhythms.

POPULATION PLAN

2,400 residents: 800 above ground and 1,600 below, across four 400-resident wards. These are new planning figures, not a previously approved census.

PUBLIC BY DEFAULT

The outdoor entrance and main underground entry welcome the public during ordinary life. Shops, school, meals and civic spaces remain active.

A SECOND DEFENSIVE LINE


The underground Welcome Hall lies before the Inner Gate Gallery. If the surface is overrun, the inhabited town can be isolated behind it.

CONSISTENT GEOMETRY

The 16 surface footprints stay where they are. New underground area IDs, vertical connections and entrances share the same Sunwell origin.

Surface connections / one joined world

New openings and passage routes / existing outdoor footprints and three crossings are preserved

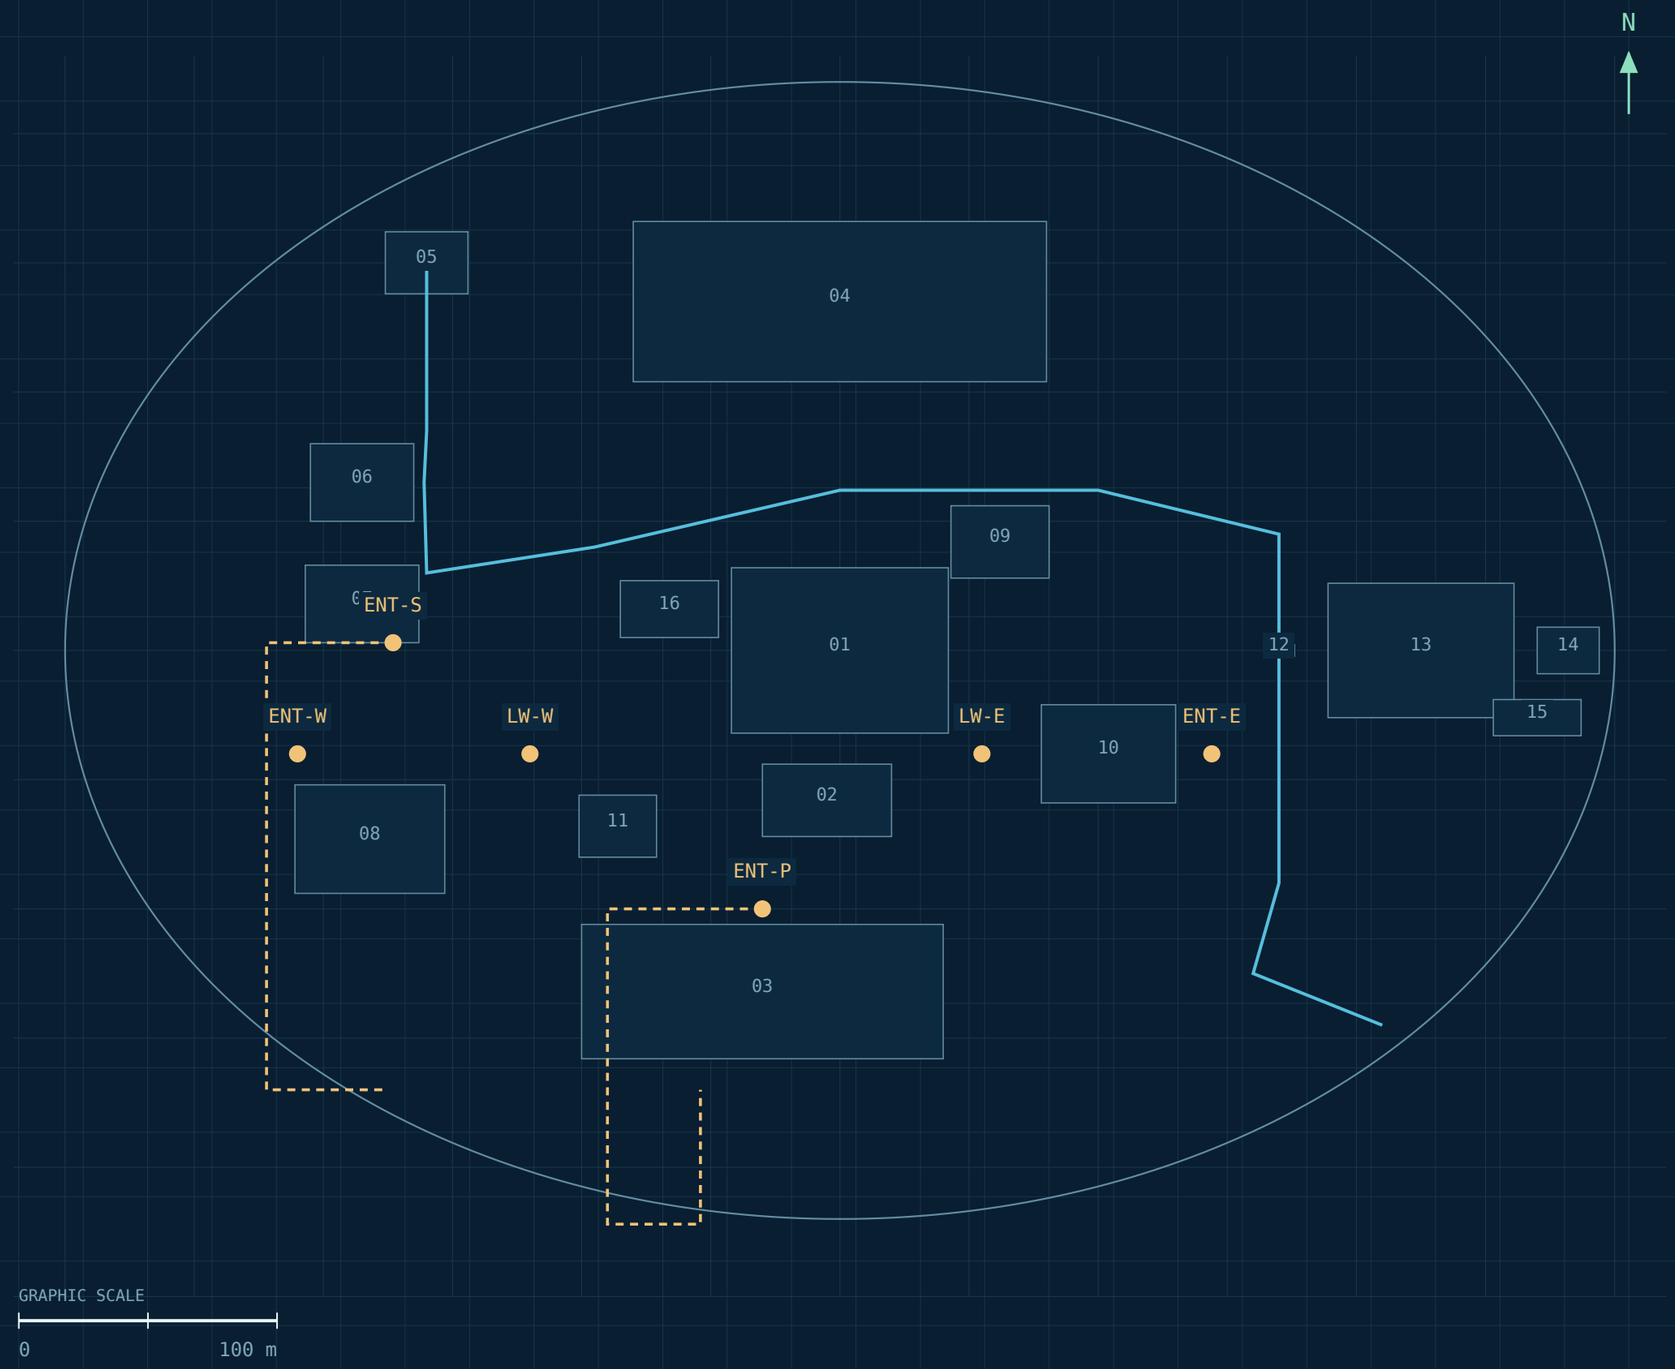

ENT-P / PUBLIC

(-30,-100,0), beneath the Hearth approach. The gallery, stairs and lift land in UG-01. The continuous step-free ramp also lands before the inner gates.

ENT-S / SERVICE

(-173,3,0), at the workshop south approach. Its ramp reaches UG-09, then the separate SG-W boundary. Deliveries never bypass the protected line.

ENT-W + ENT-E

(-210,-40,0) and (144,-40,0). Two independent stair cores link all underground levels. Controlled inward access; mechanical outward operation.

LIGHT AND AIR


LW-W and LW-E are sealed daylight ducts, not human entrances. Independent air systems and compartment controls are specified separately.

KEEP THE EXISTING MAP

All prior surface anchors, footprints, water alignment and three canal crossings remain unchanged. New openings are recorded additions.

Upper underground / homes and civic life

North-up level plan / finished floor -12 m / all coordinates share the Sunwell origin

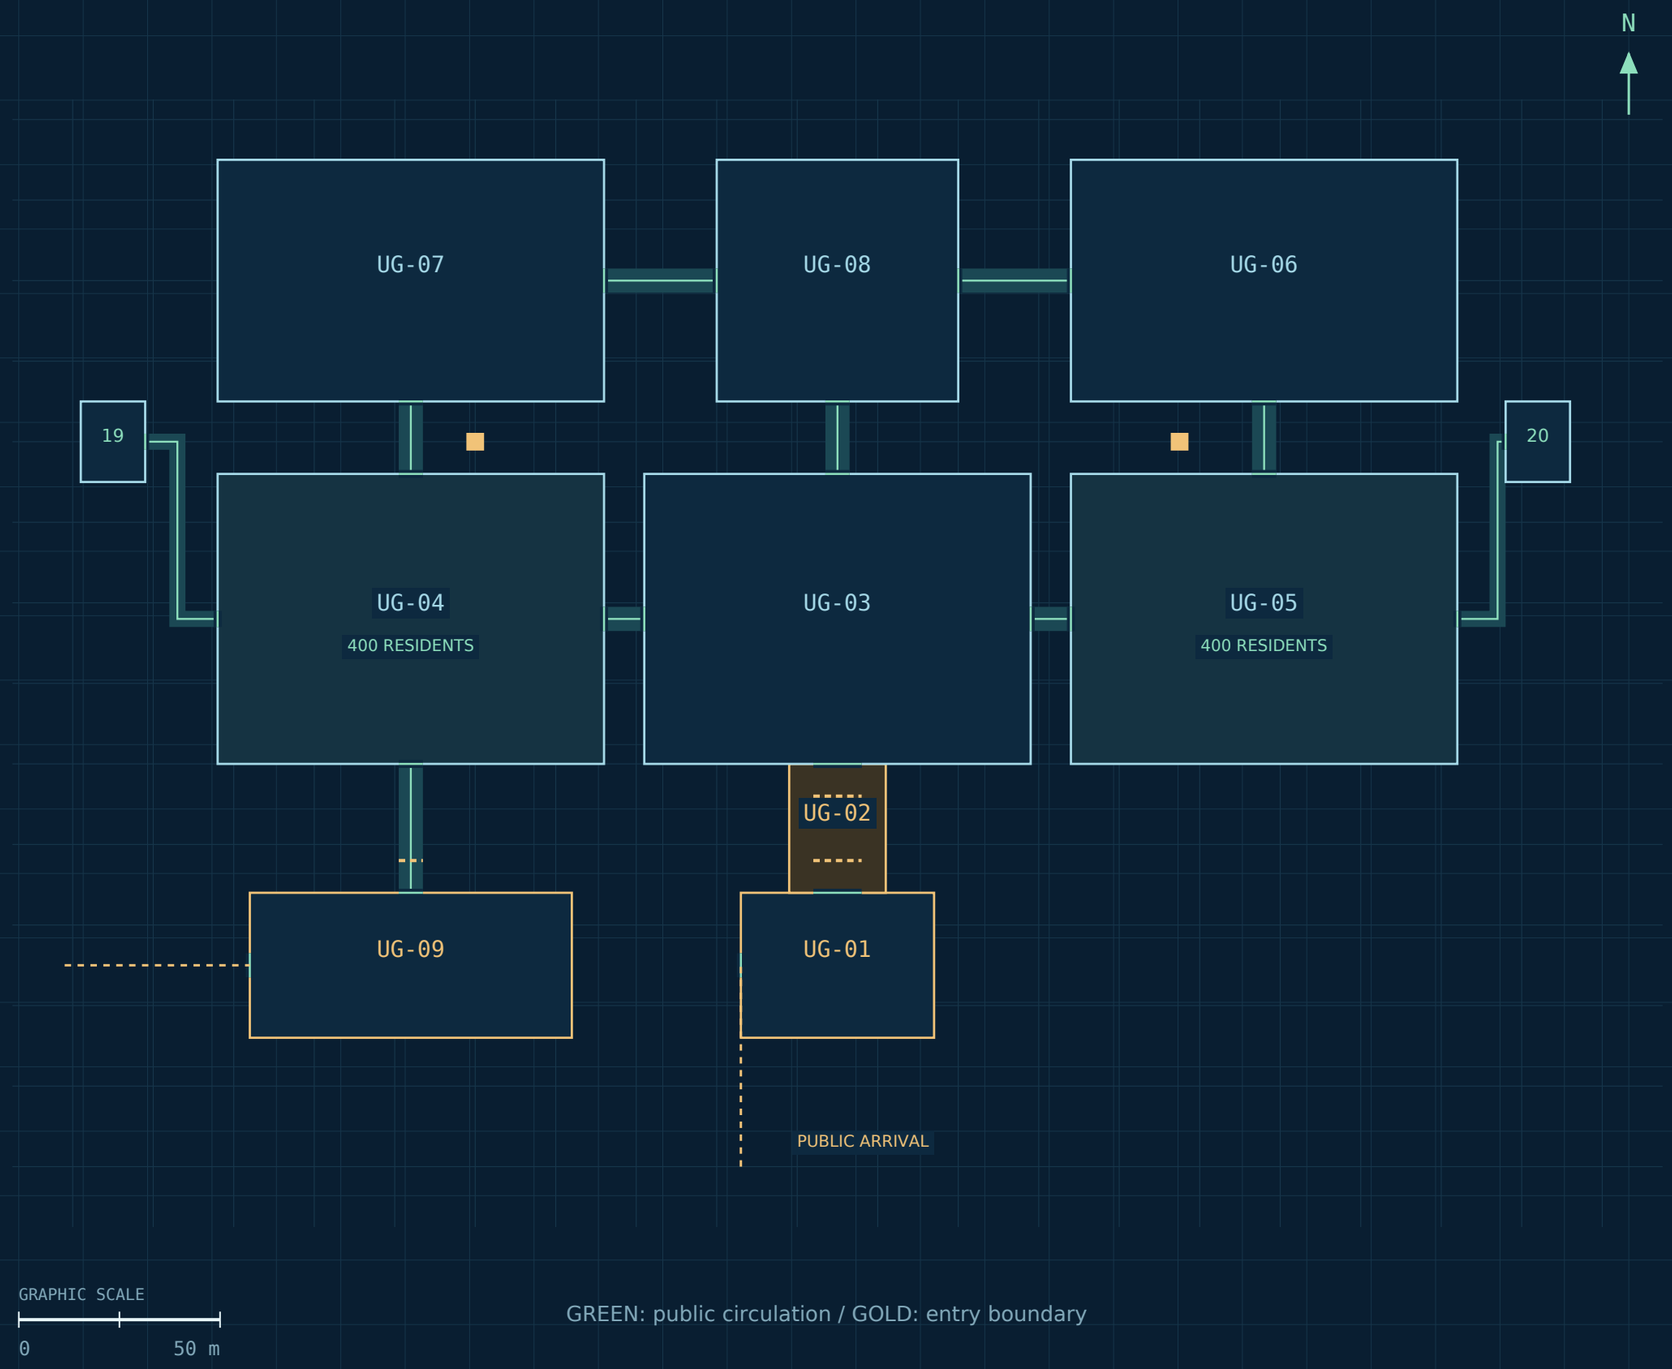

AREA REGISTER

UG-01	Welcome Hall
UG-02	Inner Gate Gallery
UG-03	Underhall Commons
UG-04	West Lantern Warren
UG-05	East Orchard Warren
UG-06	School & Play Hall
UG-07	Care & Community Hall
UG-08	Central Lift & Stair Court
UG-09	Service Receiving Hall
UG-19	West Stair & Refuge Core
UG-20	East Stair & Refuge Core


DAILY USE

800 permanent residents on this level. Welcome Hall and the service dock sit before their local protective closures; ordinary public life continues beyond.

Door-linked routes are registered in the data. Game navigation and structural details require their own implementation checks.

Deep neighborhood / homes and shared life

North-up level plan / finished floor -24 m / all coordinates share the Sunwell origin

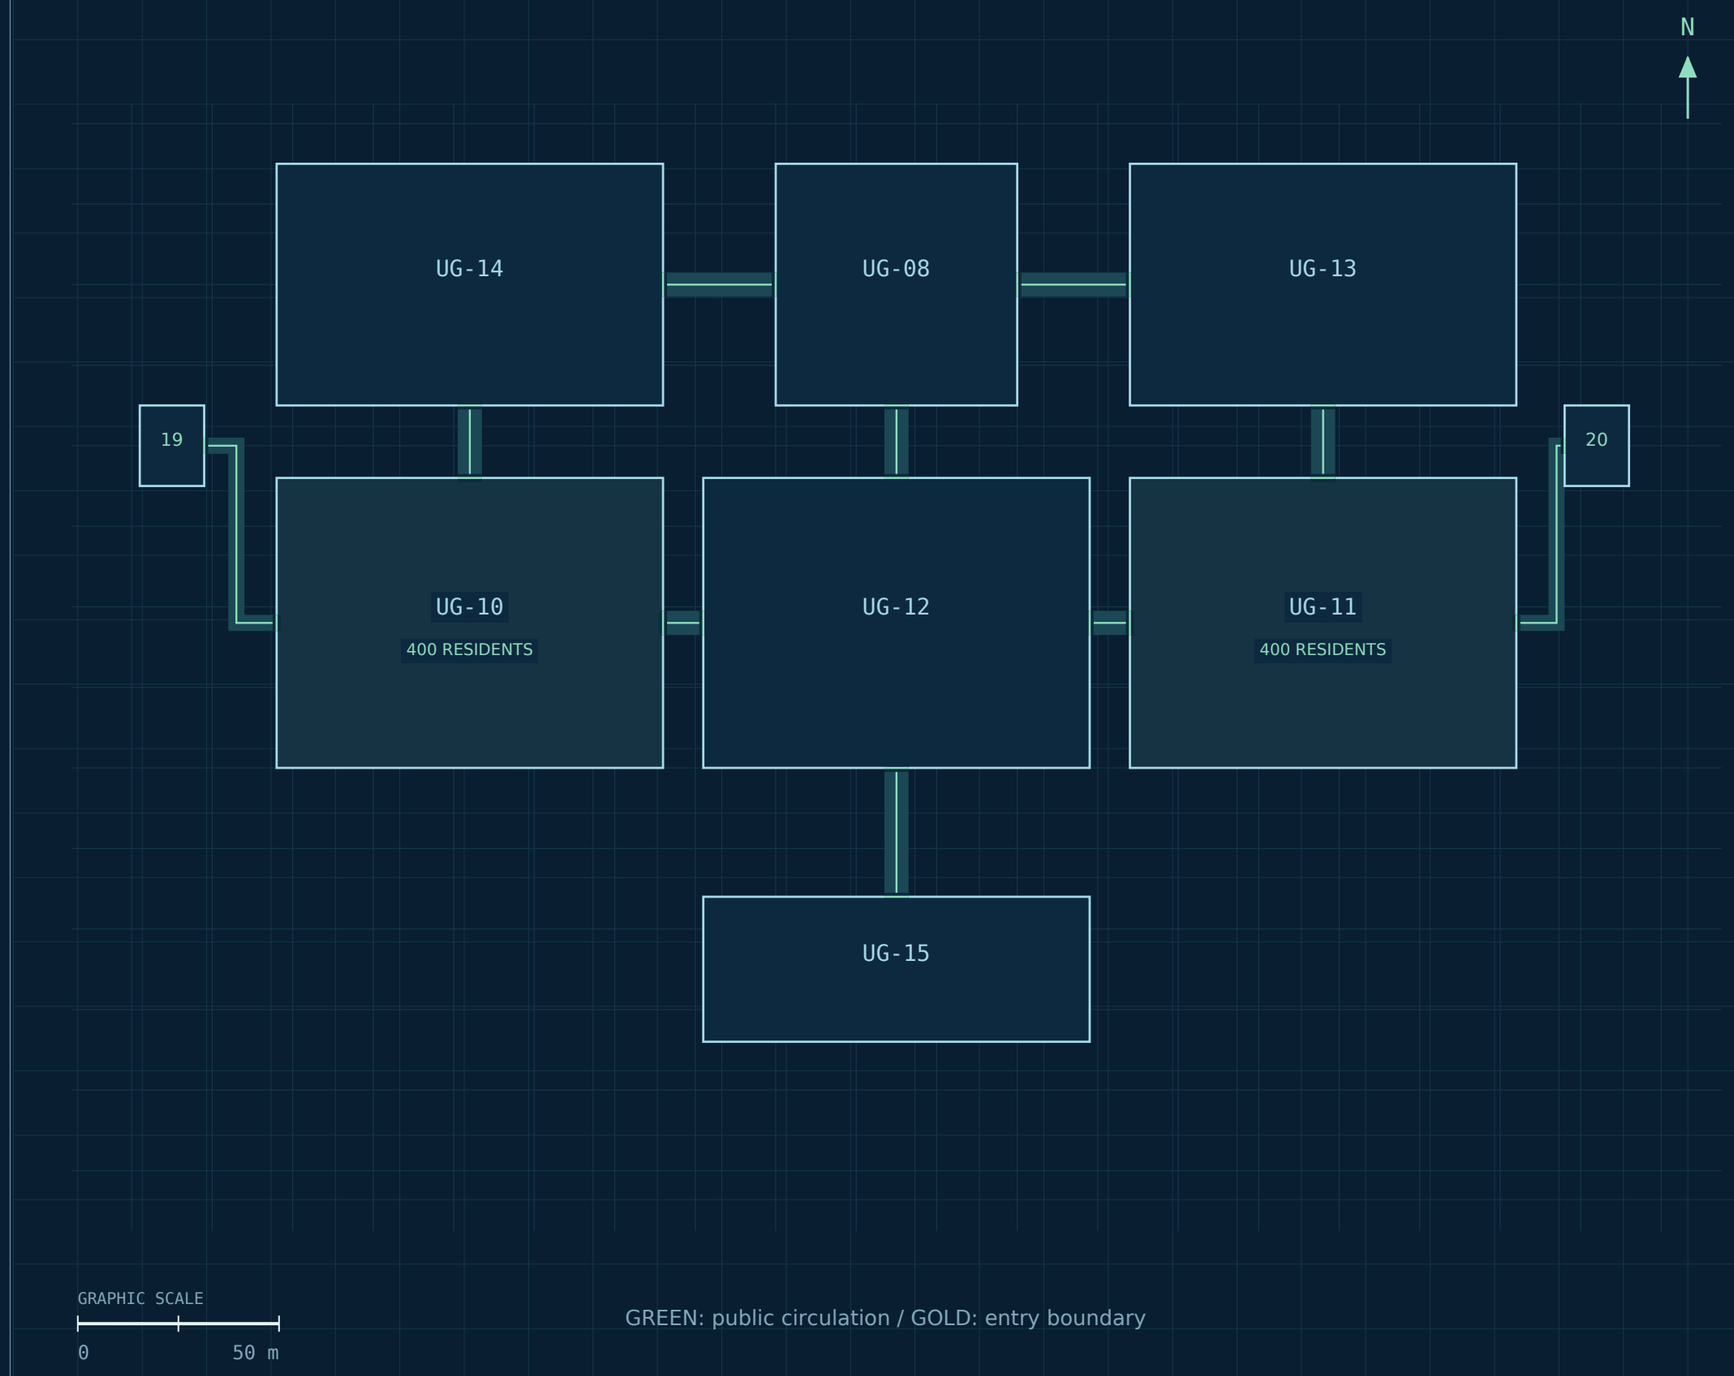

AREA REGISTER

UG-08	Central Lift & Stair Court
UG-10	West Deep Warren
UG-11	East Deep Warren
UG-12	Deep Commons & Kitchens
UG-13	Food Gardens & Grow Rooms
UG-14	Assembly & Refuge Hall
UG-15	Baths & Laundry
UG-19	West Stair & Refuge Core
UG-20	East Stair & Refuge Core


DAILY USE

800 permanent residents on this level. The assembly hall supports daily activity and a planned additional 800 refuge places for surface residents.

Door-linked routes are registered in the data. Game navigation and structural details require their own implementation checks.

Service level / maintainable infrastructure

North-up level plan / finished floor -36 m / all coordinates share the Sunwell origin

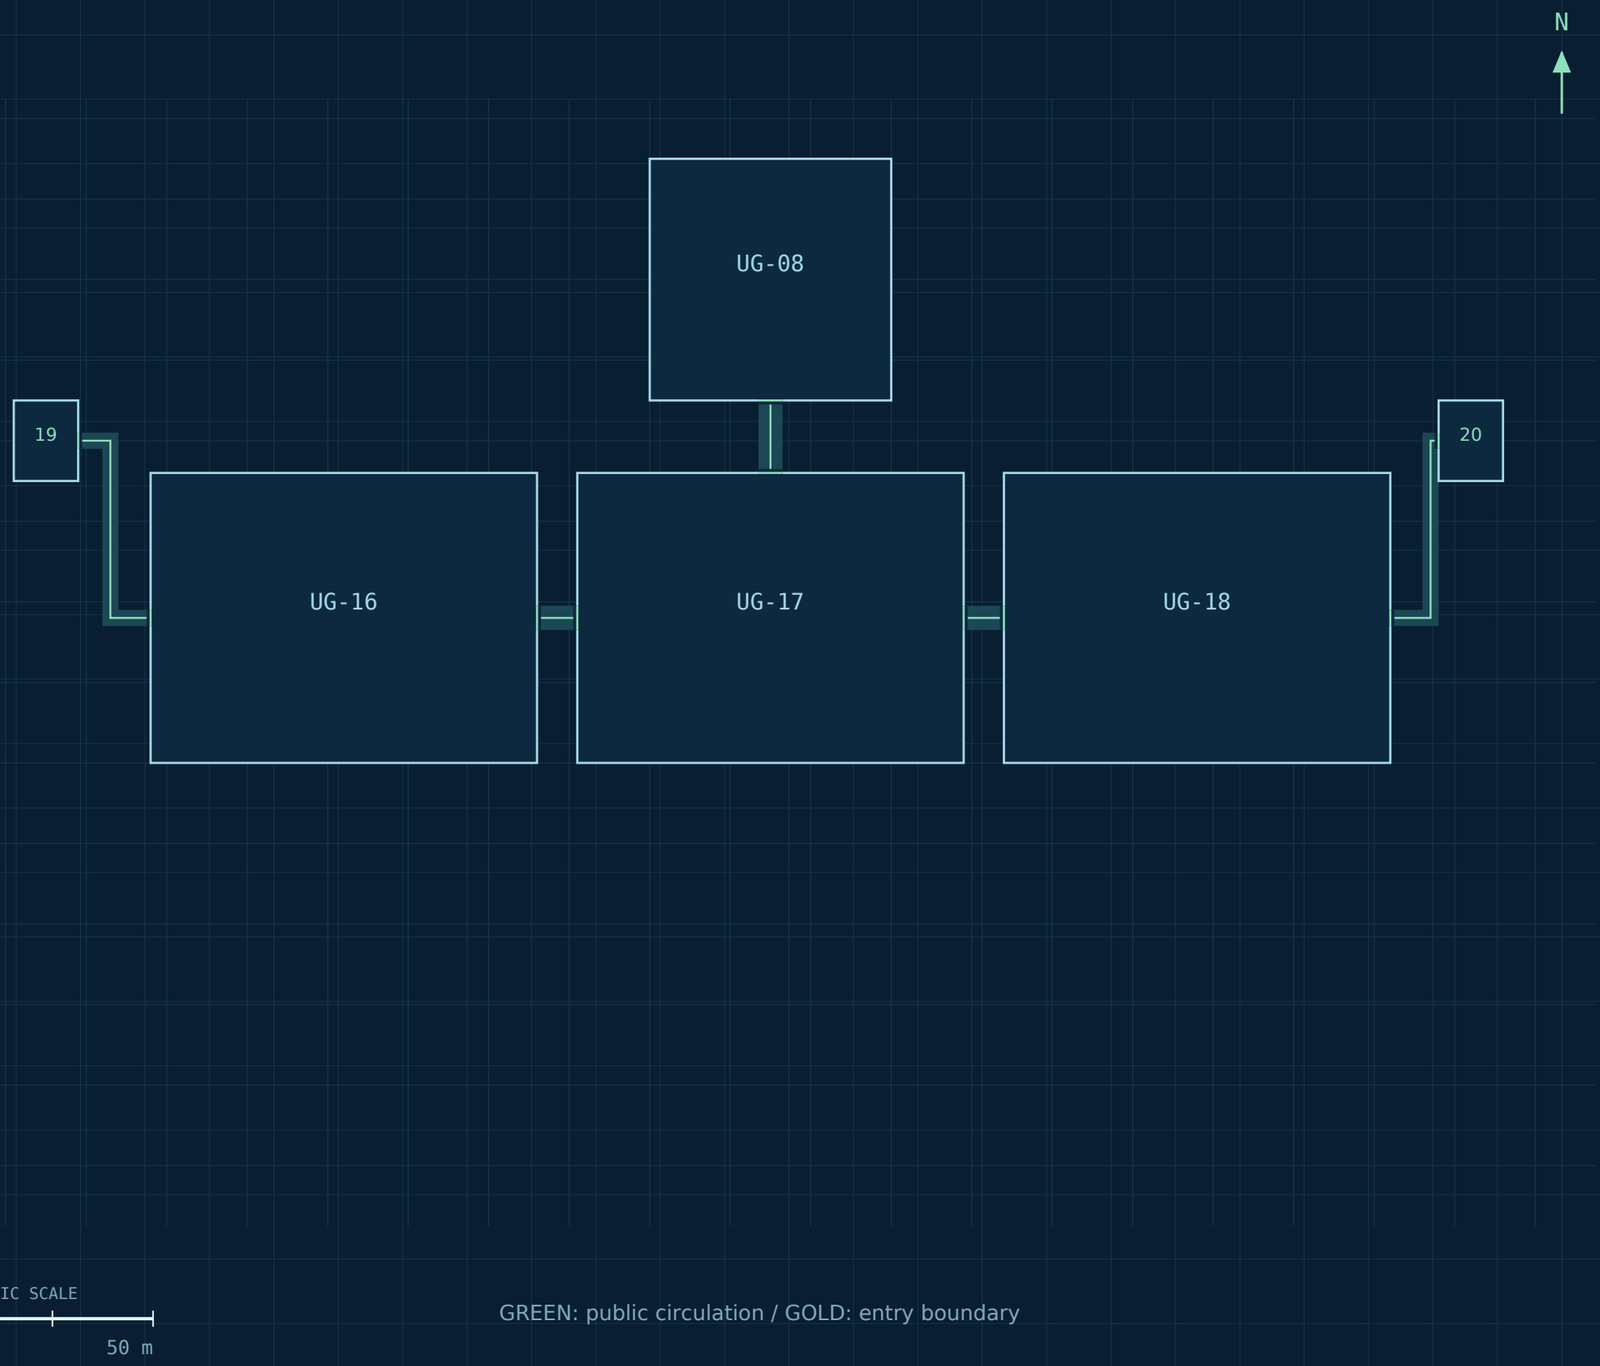

AREA REGISTER

UG-08	Central Lift & Stair Court
UG-16	Utility Repair Hall
UG-17	Water & Air Service Rooms
UG-18	Deep Stores
UG-19	West Stair & Refuge Core
UG-20	East Stair & Refuge Core

DAILY USE

Service level, with no assigned permanent homes. Separate stores, power repair, potable reserve, air handling and pumped drainage support both inhabited levels.

Door-linked routes are registered in the data. Game navigation and structural details require their own implementation checks.

Open community / protected inner town

Normal public access and a separate defensive boundary / local controls and civilian movement

01 / NORMAL DAY

Outdoor entrance open — Public welcome hall — Inner gates open — Busy homes + services

02 / PROTECTIVE TRANSITION

Guide people inward — Receive + account — Clear closure lines — Staff local boundaries

03 / SURFACE OVERRUN

Surface unsafe — Arrival zone isolated — IG-A / IG-B closed — Inner town protected

ALL SURFACE CONNECTIONS COUNT

The service dock and both stair exits have their own controlled inward thresholds. There is no unrecorded lift, hatch or tunnel that bypasses the inner boundary.

PEOPLE BEFORE CLOSURE

Stewards keep families together and confirm a gate line is clear. A busy public hall does not become an automatic trap.

LOCAL PHYSICAL CONTROL

Records can help staff, but cannot move manual bars by themselves. A network fault does not produce a universal unlock command.

TWO INDEPENDENT STAIRS

The west and east cores are separate from the central lift court. Occupants do not need network approval to exit from inside.

LIFE SUPPORT CONTINUES

Air, water, sanitation, communication and emergency lighting are zoned and locally controlled. A sealed refuge still needs working services.


REFUGE HAS A DAILY LIFE

The assembly hall hosts sport, meetings and performances. Its emergency use is an overlay, not the entire purpose of underground life.

Hearth Public Entry

Area blueprint / world anchor (-30, -144, 0) m / inherited axes, new underground area

PLAN / NORTH UP / DIMENSIONS IN METRES

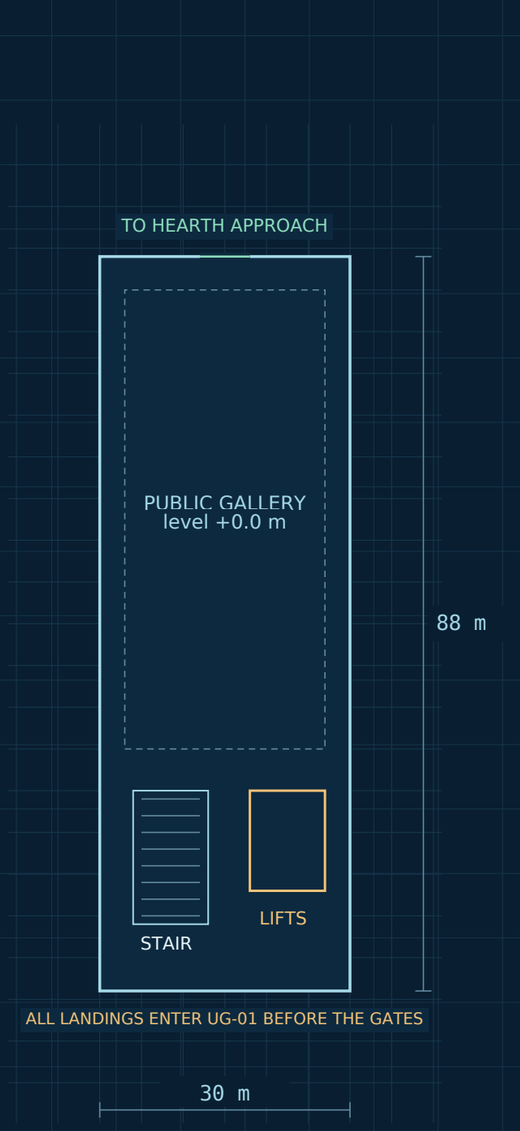

GRAPHIC SCALE


0 5 m

WORLD X = -30 + local x / Y = -144 + local y

LEVELS: 0 m

Public in ordinary life. Entry is a civic threshold, not a private club or a token-holder gate.

POSITION IN THE UNDERGROUND TOWN

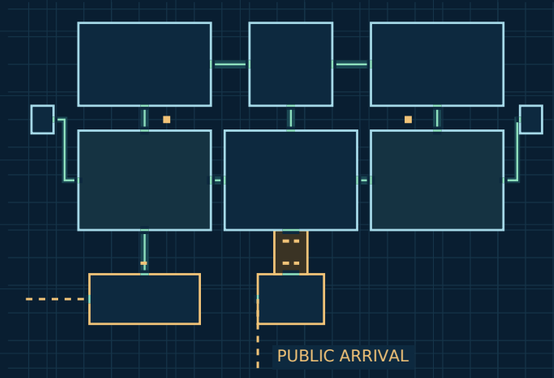

DAILY PURPOSE

A welcoming gallery below the Hearth Terraces. Public doors at (-30,-100,0) lead to lifts/stairs landing in the Welcome Hall. A continuous ramp provides a powered-lift-independent route.

CONNECTIONS / WORLD XYZ

N / 6 m clear
(-30, -100.0, 0)


Lift/stair anchor: (-30,-170), from level 0 to -12. The step-free ramp is shown on UG-A1 and recorded as a separate route.

Linework fixes area allocation, key openings and functional zones. Individual rooms and fixtures can gain further registered detail within these bounds.

Welcome Hall

Area blueprint / world anchor (-30, -170, -12) m / inherited axes, new underground area

PLAN / NORTH UP / DIMENSIONS IN METRES

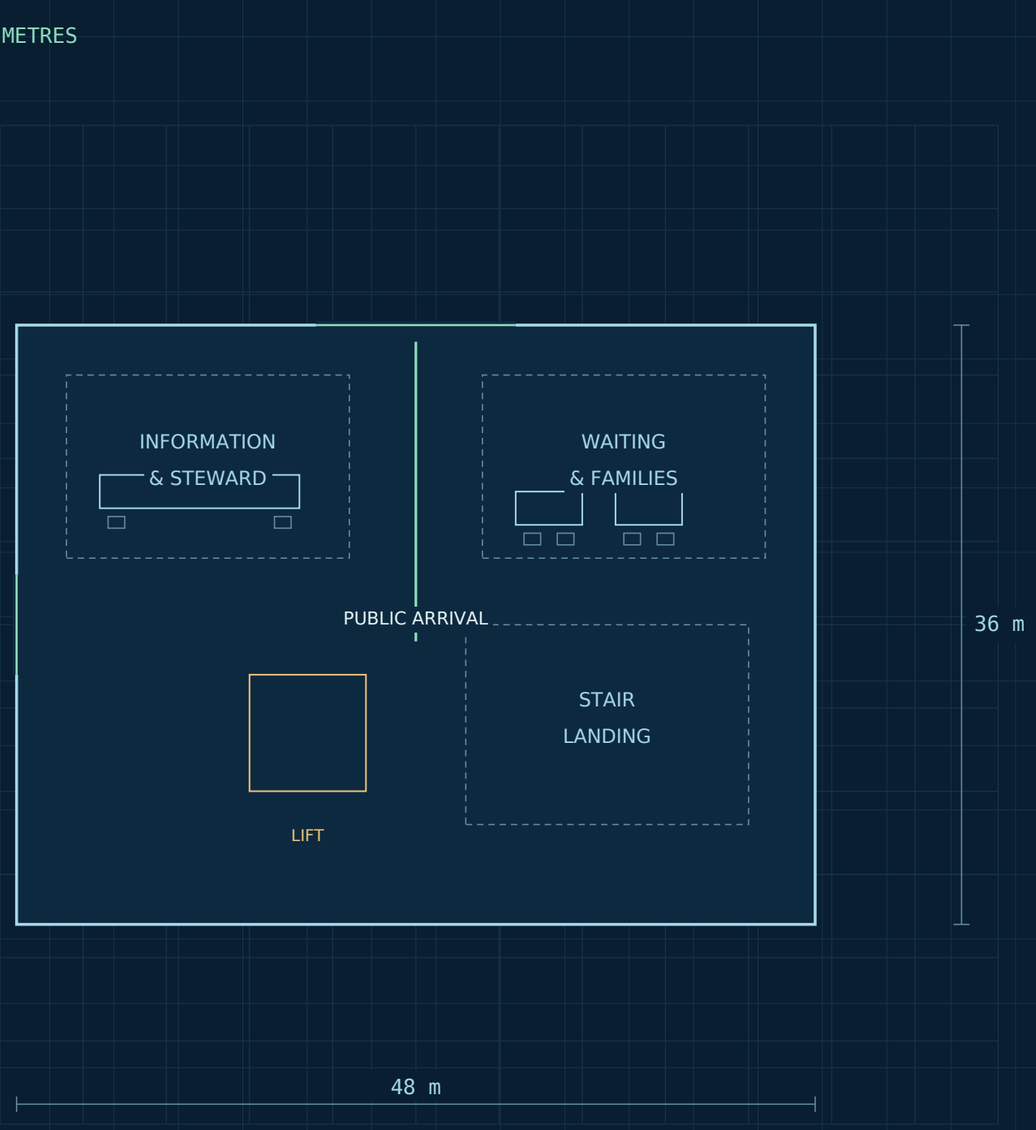

GRAPHIC SCALE


0 5 m

WORLD X = -30 + local x / Y = -170 + local y

LEVELS: -12 m

Queue space remains before the two inner closures. No lift or ramp may discharge directly behind the inner gates.

POSITION IN THE UNDERGROUND TOWN

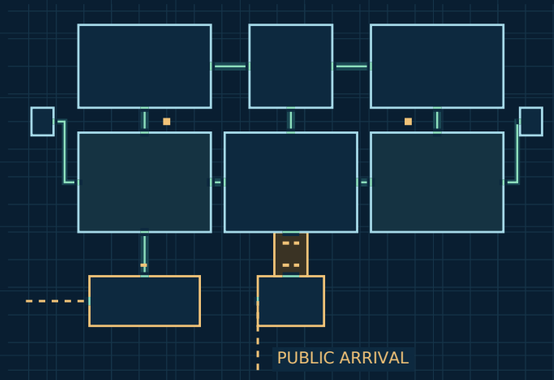

DAILY PURPOSE

The underground arrival hall: visitor information, seating, stroller/cart space and a steward desk. All main-entry routes arrive here before the inner boundary.

CONNECTIONS / WORLD XYZ

N / 12 m clear
(-30, -152.0, -12)


W / 6 m clear
(-54.0, -170, -12)

Linework fixes area allocation, key openings and functional zones. Individual rooms and fixtures can gain further registered detail within these bounds.

Inner Gate Gallery

Area blueprint / world anchor (-30, -136, -12) m / inherited axes, new underground area

PLAN / NORTH UP / DIMENSIONS IN METRES

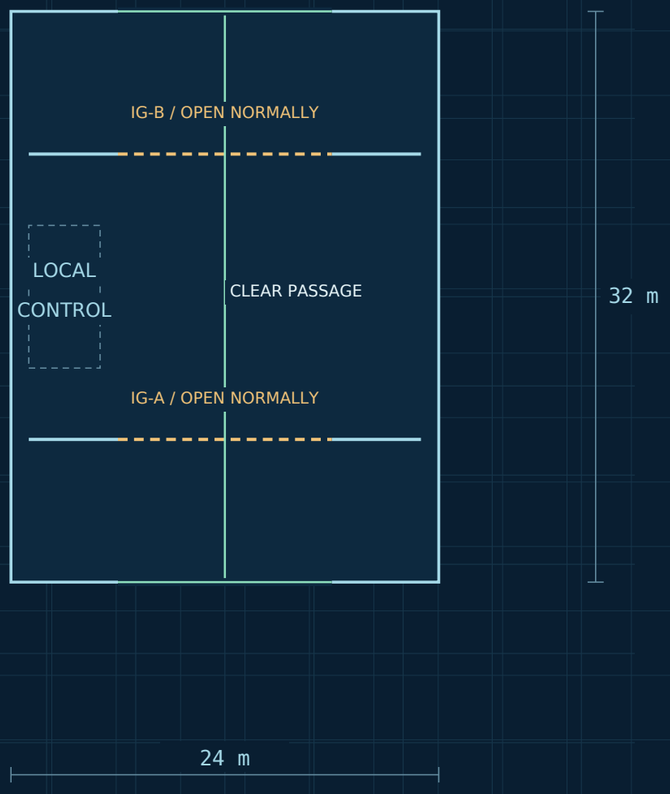

GRAPHIC SCALE


0 5 m

WORLD X = -30 + local x / Y = -136 + local y

LEVELS: -12 m

Closure lines at y=-144 and y=-128 protect the town beyond. Staff confirm people are clear; no automatic trapping of a crowded passage.

POSITION IN THE UNDERGROUND TOWN

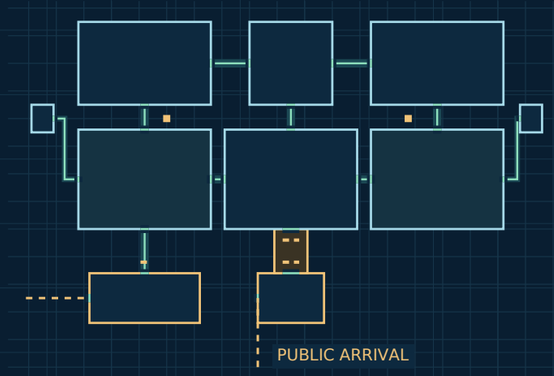

DAILY PURPOSE

A broad civic passage with two independently operated inner closures. Both are open on ordinary days.

CONNECTIONS / WORLD XYZ

S / 12 m clear
(-30, -152.0, -12)


N / 12 m clear
(-30, -120.0, -12)

Linework fixes area allocation, key openings and functional zones. Individual rooms and fixtures can gain further registered detail within these bounds.

Underhall Commons

Area blueprint / world anchor (-30, -84, -12) m / inherited axes, new underground area

PLAN / NORTH UP / DIMENSIONS IN METRES

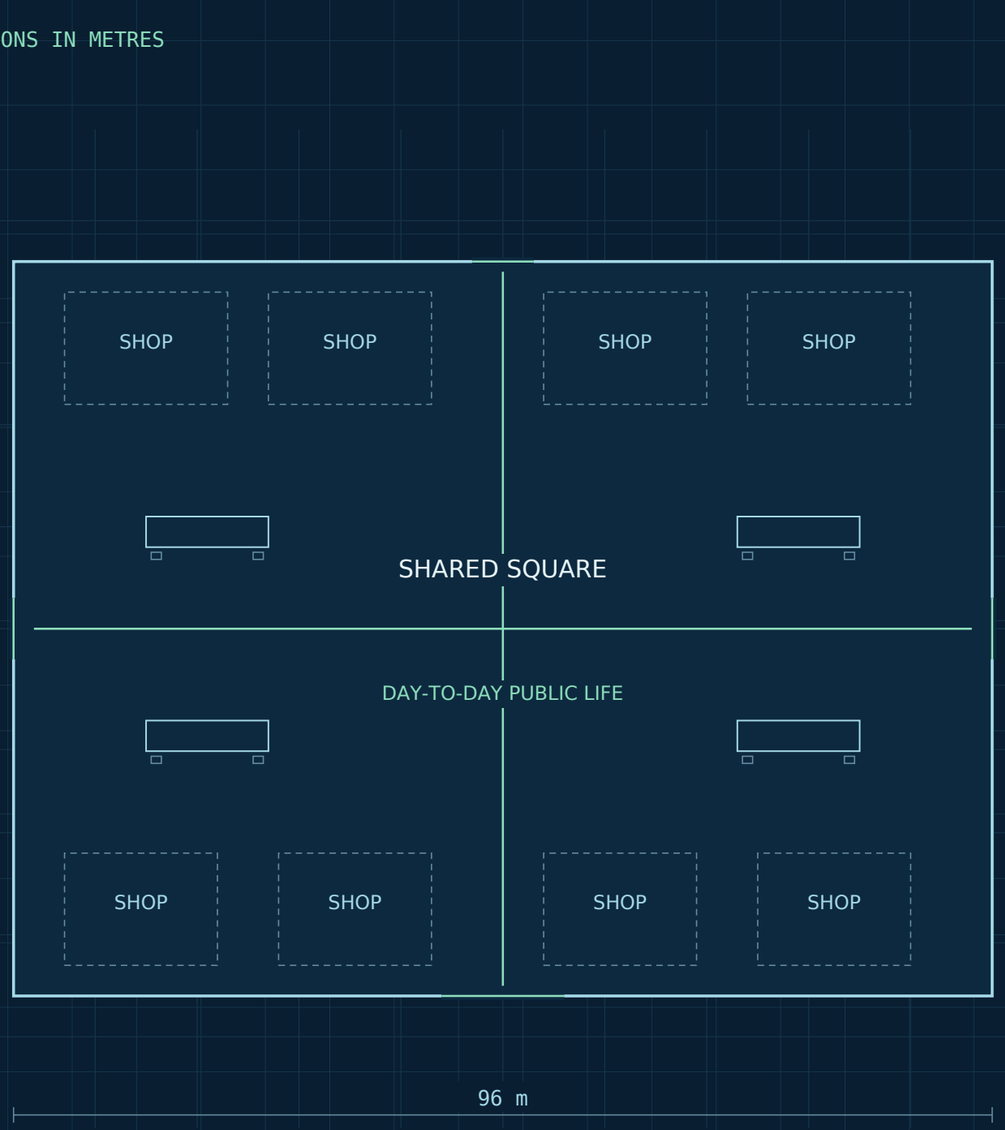

GRAPHIC SCALE


0 10 m

WORLD X = -30 + local x / Y = -84 + local y

LEVELS: -12 m

The central circulation cross stays open. This is a daily public place, not an empty bunker.

POSITION IN THE UNDERGROUND TOWN

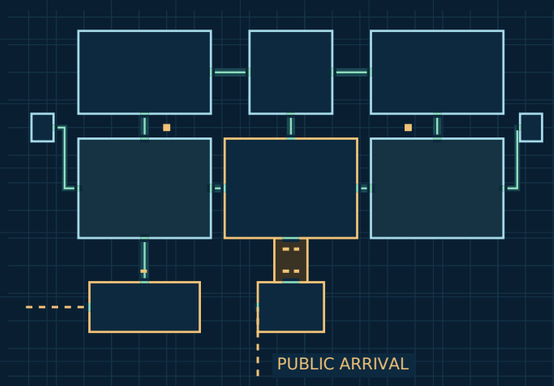

DAILY PURPOSE

A busy indoor high street with everyday shops, shared tables, a meeting square and neighborhood directions.

CONNECTIONS / WORLD XYZ

S / 12 m clear
(-30, -120.0, -12)

W / 6 m clear
(-78.0, -84, -12)

E / 6 m clear
(18.0, -84, -12)

N / 6 m clear
(-30, -48.0, -12)

Linework fixes area allocation, key openings and functional zones. Individual rooms and fixtures can gain further registered detail within these bounds.

West Lantern Warren

Area blueprint / world anchor (-136, -84, -12) m / inherited axes, new underground area

PLAN / NORTH UP / DIMENSIONS IN METRES



GRAPHIC SCALE


0 10 m

WORLD X = -136 + local x / Y = -84 + local y

LEVELS: -12 m

Lantern is a neighborhood name and ordinary lighting; no magical energy object. Private room layouts stay unassigned until drawn.

POSITION IN THE UNDERGROUND TOWN

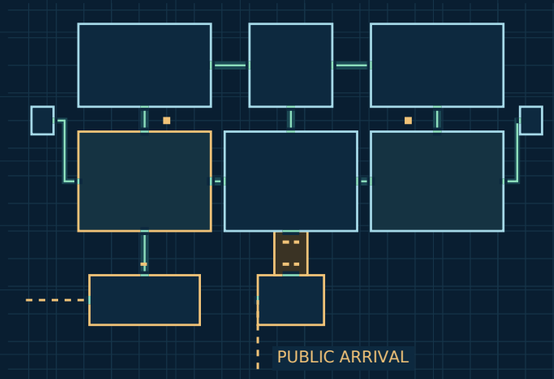

DAILY PURPOSE

Four household courts, shared play rooms, deliveries, doorways, kitchens and quiet residential galleries. Planning occupancy: 400 residents / 100 homes.

CONNECTIONS / WORLD XYZ

E / 6 m clear
(-88.0, -84, -12)

N / 6 m clear
(-136, -48.0, -12)

S / 6 m clear
(-136, -120.0, -12)

W / 4 m clear
(-184.0, -84, -12)

Linework fixes area allocation, key openings and functional zones. Individual rooms and fixtures can gain further registered detail within these bounds.

East Orchard Warren

Area blueprint / world anchor (76, -84, -12) m / inherited axes, new underground area

PLAN / NORTH UP / DIMENSIONS IN METRES



GRAPHIC SCALE


0 10 m

WORLD X = 76 + local x / Y = -84 + local y

LEVELS: -12 m

Plants are decorative and locally grown; they do not imply unlimited daylight or a self-feeding town.

POSITION IN THE UNDERGROUND TOWN

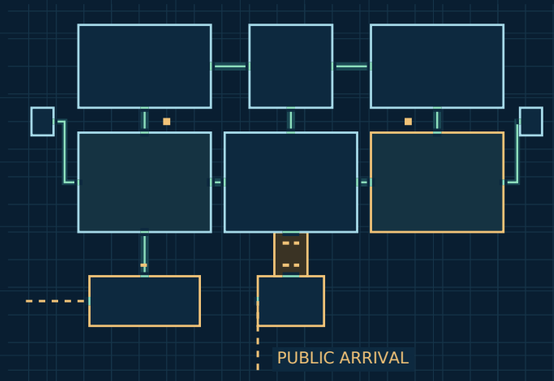

DAILY PURPOSE

Four dense residential courts with family homes, planted gathering pockets and neighbor-run shops. Planning occupancy: 400 residents / 100 homes.

CONNECTIONS / WORLD XYZ

W / 6 m clear
(28.0, -84, -12)

N / 6 m clear
(76, -48.0, -12)


E / 4 m clear
(124.0, -84, -12)

Linework fixes area allocation, key openings and functional zones. Individual rooms and fixtures can gain further registered detail within these bounds.

School & Play Hall

Area blueprint / world anchor (76, 0, -12) m / inherited axes, new underground area

PLAN / NORTH UP / DIMENSIONS IN METRES

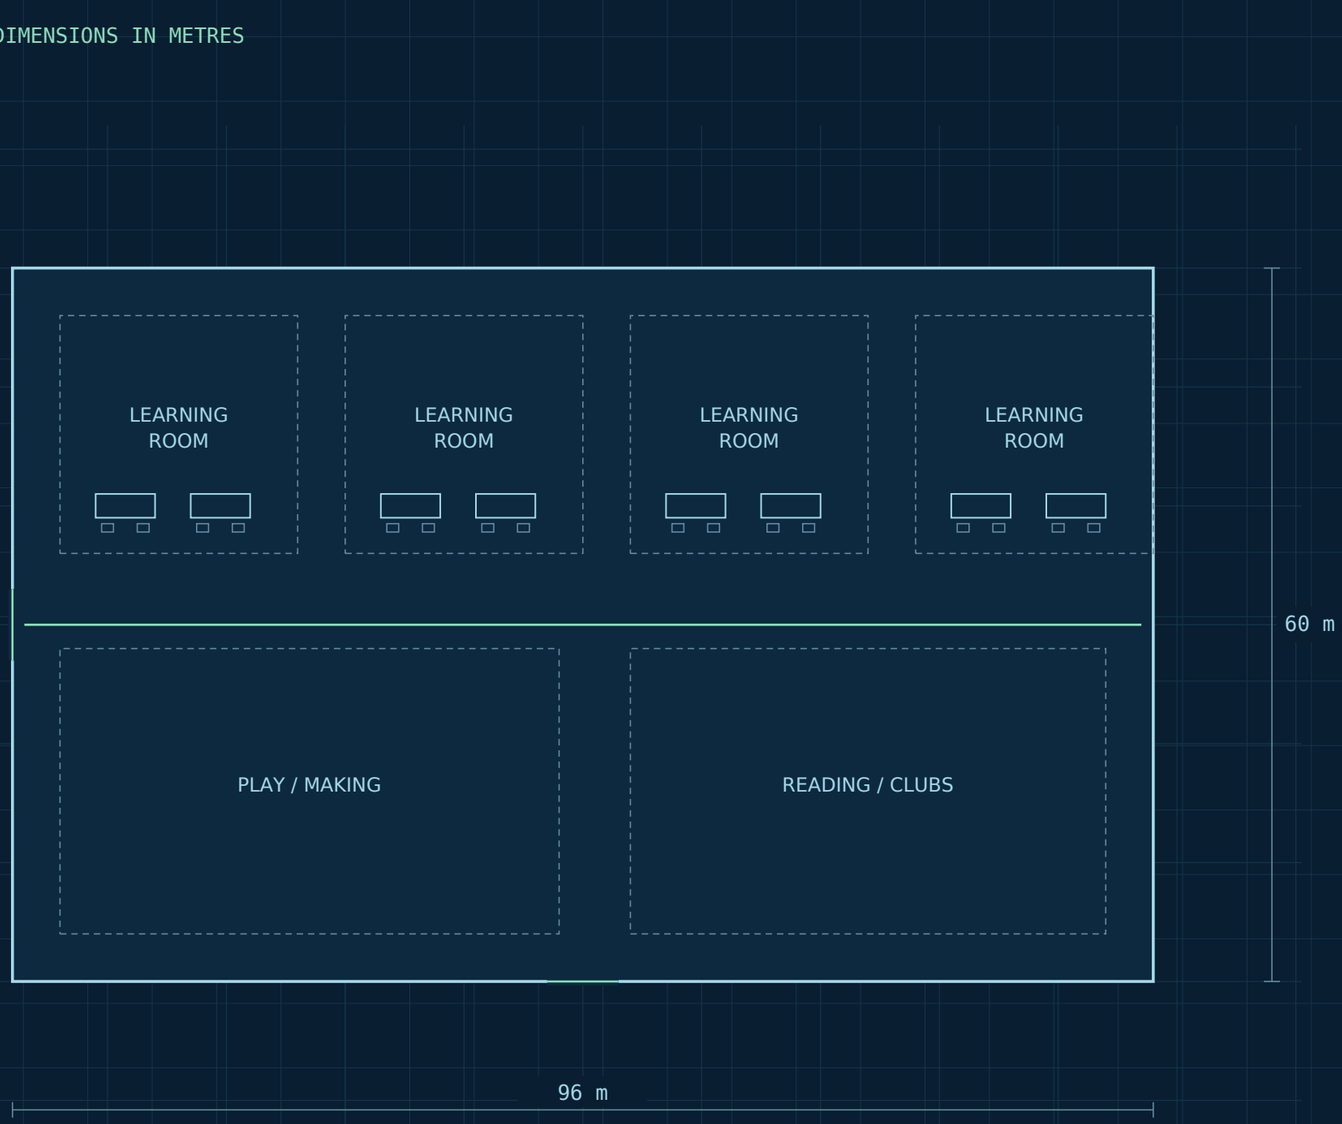

GRAPHIC SCALE


0 10 m

WORLD X = 76 + local x / Y = 0 + local y

LEVELS: -12 m

Children retain ordinary routines and protected gathering areas; danger does not turn the school into a combat room.

POSITION IN THE UNDERGROUND TOWN

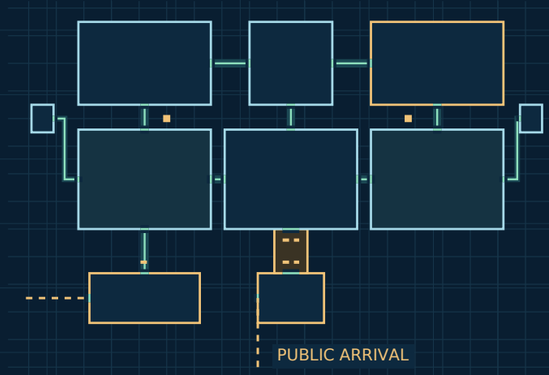

DAILY PURPOSE

Classrooms, reading, supervised play, making and community learning used by children from both surface and underground homes.

CONNECTIONS / WORLD XYZ

S / 6 m clear
(76, -30.0, -12)


W / 6 m clear
(28.0, 0, -12)

Linework fixes area allocation, key openings and functional zones. Individual rooms and fixtures can gain further registered detail within these bounds.

Care & Community Hall

Area blueprint / world anchor (-136, 0, -12) m / inherited axes, new underground area

PLAN / NORTH UP / DIMENSIONS IN METRES

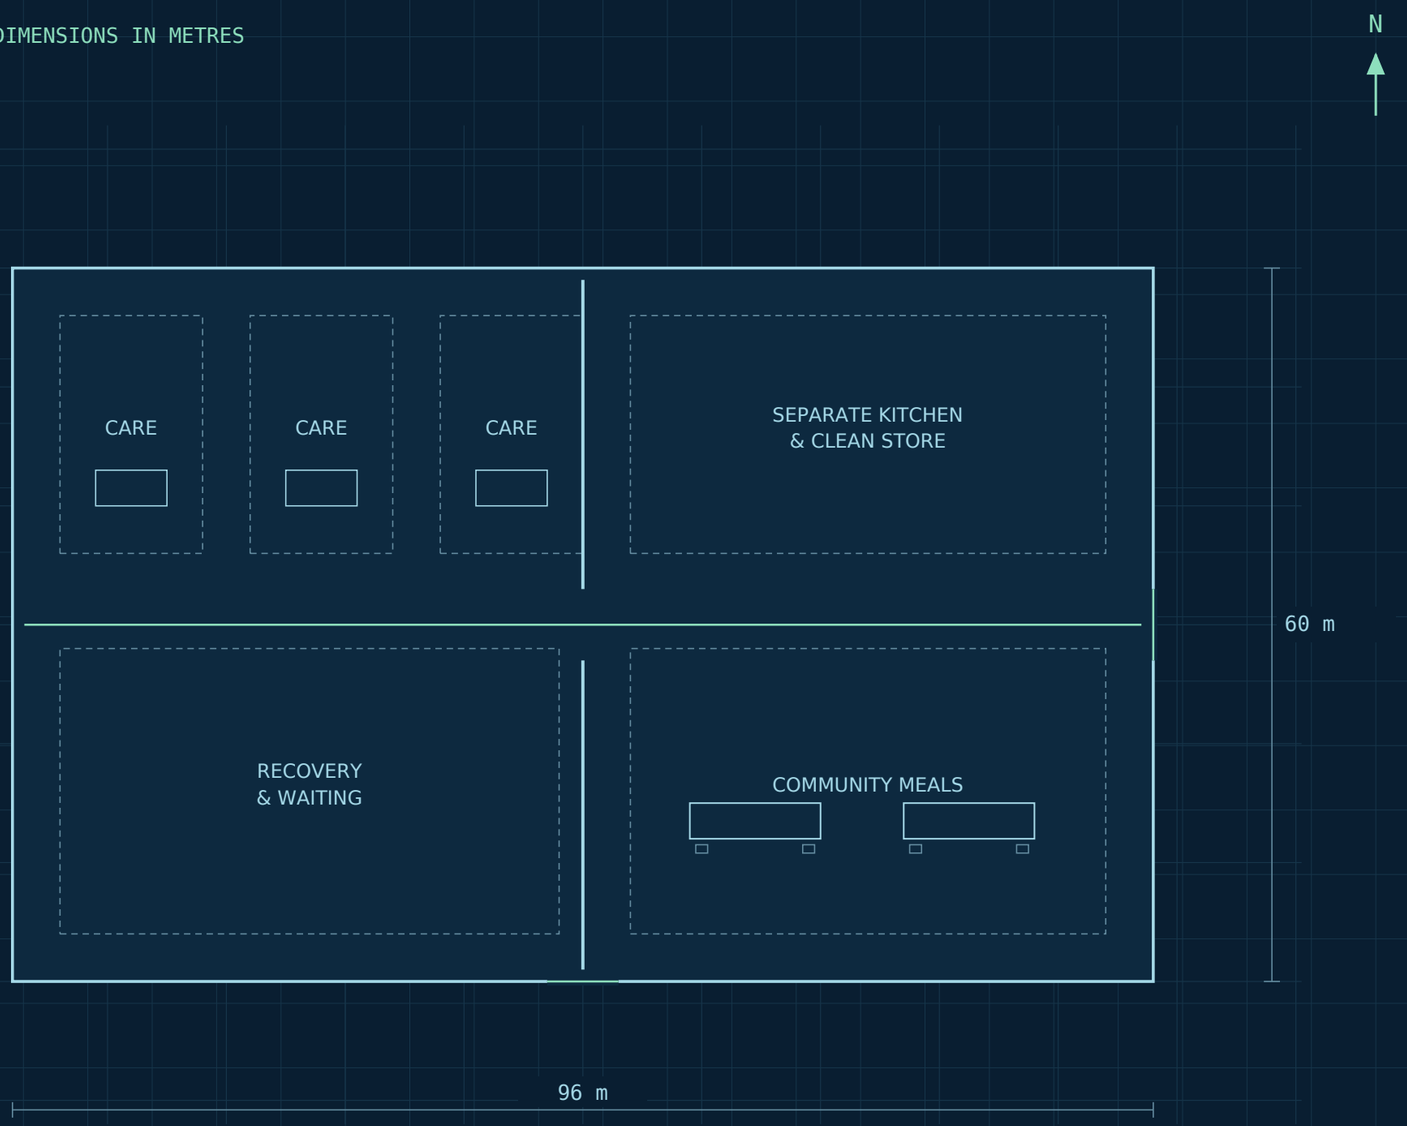

GRAPHIC SCALE


0 10 m

WORLD X = -136 + local x / Y = 0 + local y

LEVELS: -12 m

Clinical rooms remain private. Kitchen noise and deliveries stay outside the care-room aisle.

POSITION IN THE UNDERGROUND TOWN

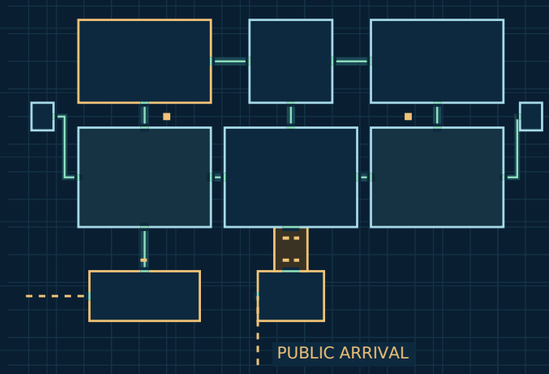

DAILY PURPOSE

Clinic rooms, recovery, community meals and a separate kitchen wing, with independent clean and service circulation.

CONNECTIONS / WORLD XYZ

S / 6 m clear
(-136, -30.0, -12)

E / 6 m clear
(-88.0, 0, -12)

Linework fixes area allocation, key openings and functional zones. Individual rooms and fixtures can gain further registered detail within these bounds.

Central Lift & Stair Court

Area blueprint / world anchor (-30, 0, -12) m / inherited axes, new underground area

PLAN / NORTH UP / DIMENSIONS IN METRES



GRAPHIC SCALE


0 5 m

WORLD X = -30 + local x / Y = 0 + local y

LEVELS: -12 m, -24 m, -36 m

This core has no direct surface entrance. It connects only the protected side of the underground town.

POSITION IN THE UNDERGROUND TOWN

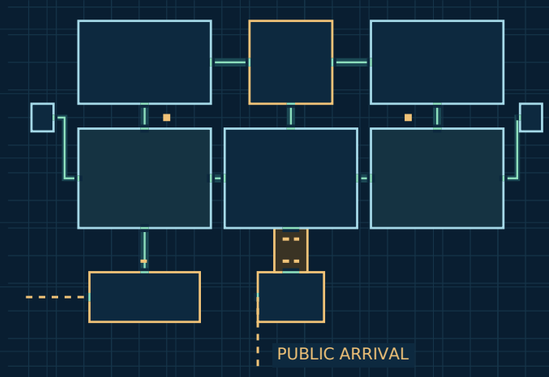

DAILY PURPOSE

A stacked neighborhood interchange at -12, -24 and -36 m, with ordinary lifts and independent stairs.

CONNECTIONS / WORLD XYZ

S / 6 m clear
(-30, -30.0, -12)

W / 6 m clear
(-60.0, 0, -12)

E / 6 m clear
(0.0, 0, -12)

The same horizontal footprint and matching landings repeat at -12, -24 and -36 m. Stairs are independent of powered lifts.

Linework fixes area allocation, key openings and functional zones. Individual rooms and fixtures can gain further registered detail within these bounds.

Service Receiving Hall

Area blueprint / world anchor (-136, -170, -12) m / inherited axes, new underground area

PLAN / NORTH UP / DIMENSIONS IN METRES



GRAPHIC SCALE


0 10 m

WORLD X = -136 + local x / Y = -170 + local y

LEVELS: -12 m

The dock gate is a separate surface-to-town defensive boundary; it cannot be left as an unguarded bypass.

POSITION IN THE UNDERGROUND TOWN

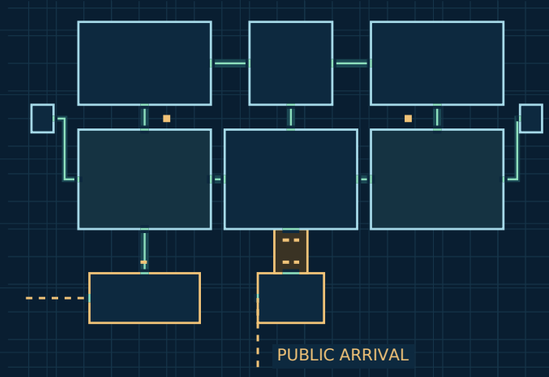

DAILY PURPOSE

Freight from the workshop service passage is checked, staged and handed into the west neighborhood through a local closure.

CONNECTIONS / WORLD XYZ

N / 6 m clear
(-136, -152.0, -12)

W / 6 m clear
(-176.0, -170, -12)

Linework fixes area allocation, key openings and functional zones. Individual rooms and fixtures can gain further registered detail within these bounds.

West Deep Warren

Area blueprint / world anchor (-136, -84, -24) m / inherited axes, new underground area

PLAN / NORTH UP / DIMENSIONS IN METRES



GRAPHIC SCALE


0 10 m

WORLD X = -136 + local x / Y = -84 + local y

LEVELS: -24 m

Depth is not a class hierarchy. These residents use surface gardens, markets and celebrations daily.

POSITION IN THE UNDERGROUND TOWN

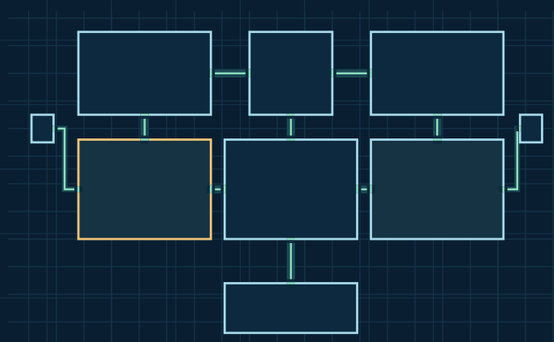

DAILY PURPOSE

A second residential neighborhood, equal in dignity and quality to the upper warren. Planning occupancy: 400 residents / 100 homes.

CONNECTIONS / WORLD XYZ

E / 6 m clear
(-88.0, -84, -24)

N / 6 m clear
(-136, -48.0, -24)

W / 4 m clear
(-184.0, -84, -24)

Linework fixes area allocation, key openings and functional zones. Individual rooms and fixtures can gain further registered detail within these bounds.

East Deep Warren

Area blueprint / world anchor (76, -84, -24) m / inherited axes, new underground area

PLAN / NORTH UP / DIMENSIONS IN METRES



GRAPHIC SCALE


0 10 m

WORLD X = 76 + local x / Y = -84 + local y

LEVELS: -24 m

The four wards are normal permanent homes, not temporary emergency beds.

POSITION IN THE UNDERGROUND TOWN

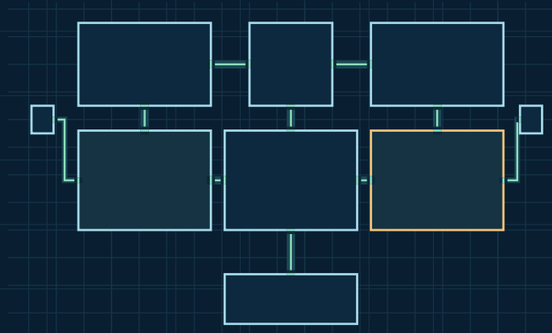

DAILY PURPOSE

Dense family courtyards, homes, doorstep shops and social galleries on the second inhabited level. Planning occupancy: 400 residents / 100 homes.

CONNECTIONS / WORLD XYZ

W / 6 m clear
(28.0, -84, -24)

N / 6 m clear
(76, -48.0, -24)

E / 4 m clear
(124.0, -84, -24)

Linework fixes area allocation, key openings and functional zones. Individual rooms and fixtures can gain further registered detail within these bounds.

Deep Commons & Kitchens

Area blueprint / world anchor (-30, -84, -24) m / inherited axes, new underground area

PLAN / NORTH UP / DIMENSIONS IN METRES



GRAPHIC SCALE


0 10 m

WORLD X = -30 + local x / Y = -84 + local y

LEVELS: -24 m

Keep food preparation, clean stores and waste handling distinct. Household kitchens also exist.

POSITION IN THE UNDERGROUND TOWN

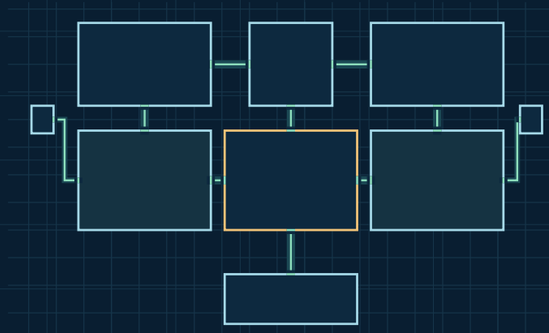

DAILY PURPOSE

A shared meal hall, neighborhood shops and kitchens beside the lower residential streets.

CONNECTIONS / WORLD XYZ

W / 6 m clear
(-78.0, -84, -24)

E / 6 m clear
(18.0, -84, -24)

N / 6 m clear
(-30, -48.0, -24)

S / 6 m clear
(-30, -120.0, -24)

Linework fixes area allocation, key openings and functional zones. Individual rooms and fixtures can gain further registered detail within these bounds.

Food Gardens & Grow Rooms

Area blueprint / world anchor (76, 0, -24) m / inherited axes, new underground area

PLAN / NORTH UP / DIMENSIONS IN METRES



GRAPHIC SCALE


0 10 m

WORLD X = 76 + local x / Y = 0 + local y

LEVELS: -24 m

Grow lights require power. Underground cultivation supplements surface gardens and external trade; it does not feed everybody alone.

POSITION IN THE UNDERGROUND TOWN

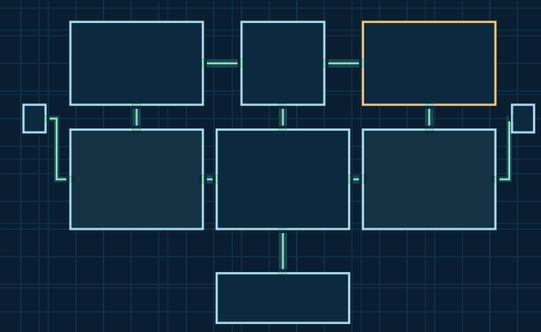

DAILY PURPOSE

Powered growing rooms, seed storage and food preparation for selected greens, herbs and plant starts.

CONNECTIONS / WORLD XYZ

S / 6 m clear
(76, -30.0, -24)


W / 6 m clear
(28.0, 0, -24)

Linework fixes area allocation, key openings and functional zones. Individual rooms and fixtures can gain further registered detail within these bounds.

Assembly & Refuge Hall

Area blueprint / world anchor (-136, 0, -24) m / inherited axes, new underground area

PLAN / NORTH UP / DIMENSIONS IN METRES

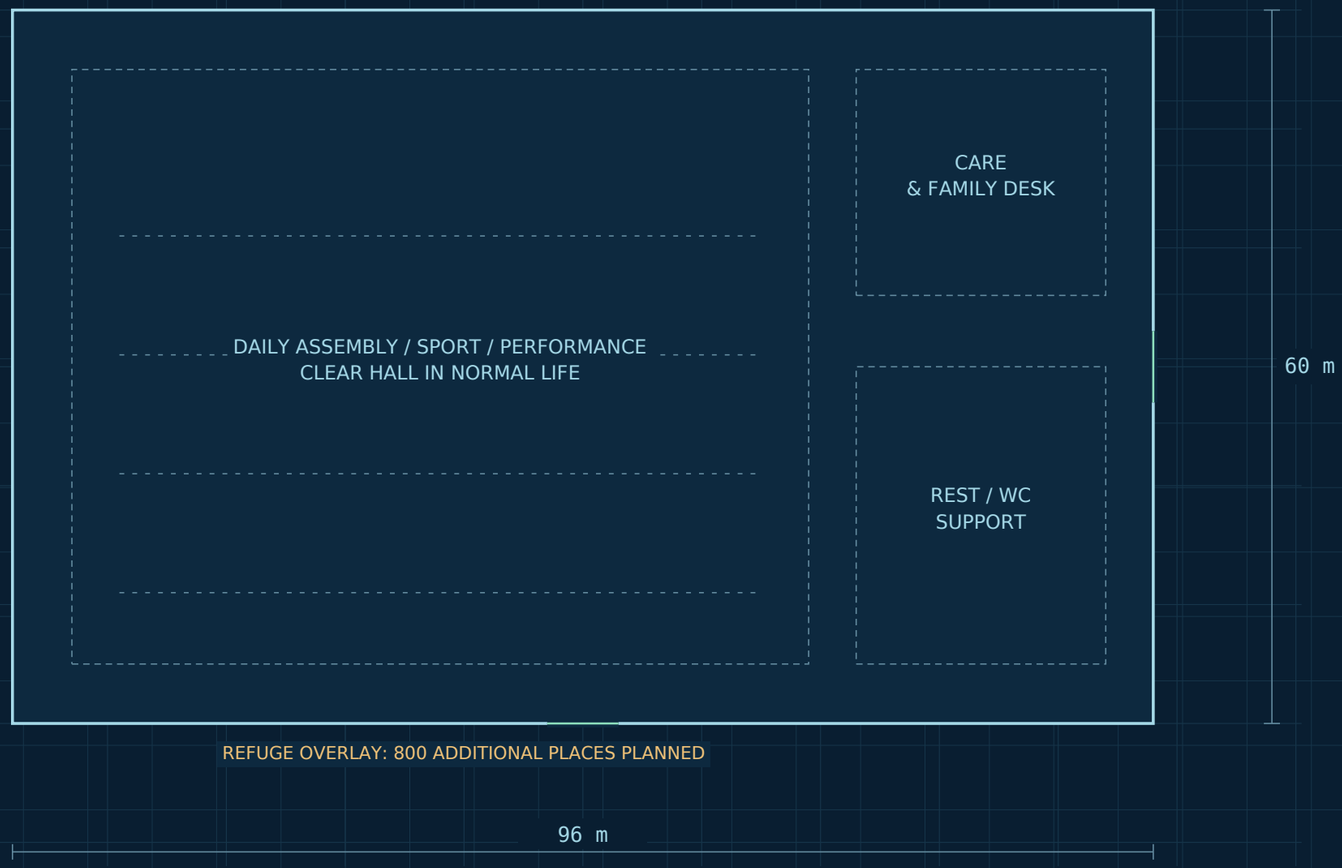

GRAPHIC SCALE


0 10 m

WORLD X = -136 + local x / Y = 0 + local y

LEVELS: -24 m

800 additional refuge places is a production planning target, not a certified capacity. Do not displace underground households to make refuge space.

POSITION IN THE UNDERGROUND TOWN

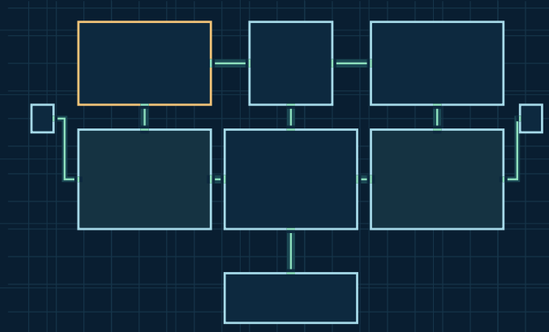

DAILY PURPOSE

Used daily for gatherings, sport, performances and clubs. In a protective state it receives surface residents, with rest, care and family reunification zones.

CONNECTIONS / WORLD XYZ

S / 6 m clear
(-136, -30.0, -24)


E / 6 m clear
(-88.0, 0, -24)

Linework fixes area allocation, key openings and functional zones. Individual rooms and fixtures can gain further registered detail within these bounds.

Baths & Laundry

Area blueprint / world anchor (-30, -170, -24) m / inherited axes, new underground area

PLAN / NORTH UP / DIMENSIONS IN METRES

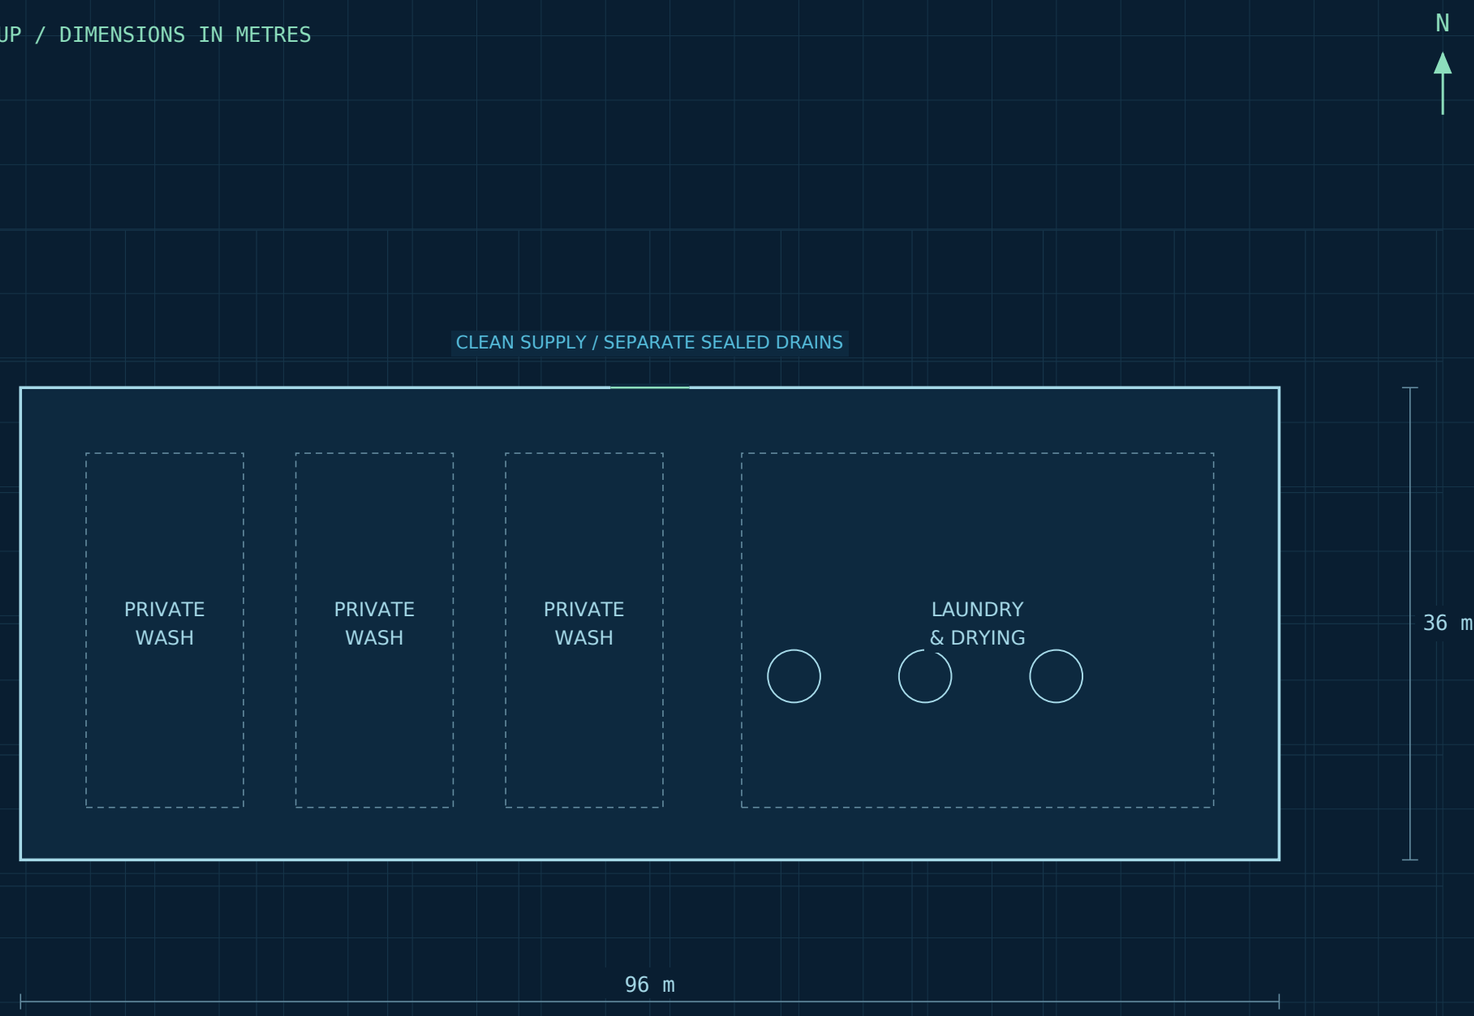

GRAPHIC SCALE


0 10 m

WORLD X = -30 + local x / Y = -170 + local y

LEVELS: -24 m

Separate clean water from drainage. No connection opens through the Welcome Hall above.

POSITION IN THE UNDERGROUND TOWN

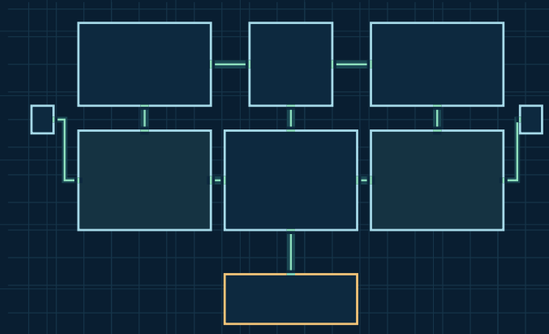

DAILY PURPOSE

Shared baths, private washing rooms, laundry, drying and neighborhood maintenance stores.

CONNECTIONS / WORLD XYZ


N / 6 m clear
(-30, -152.0, -24)

Linework fixes area allocation, key openings and functional zones. Individual rooms and fixtures can gain further registered detail within these bounds.

Utility Repair Hall

Area blueprint / world anchor (-136, -84, -36) m / inherited axes, new underground area

PLAN / NORTH UP / DIMENSIONS IN METRES

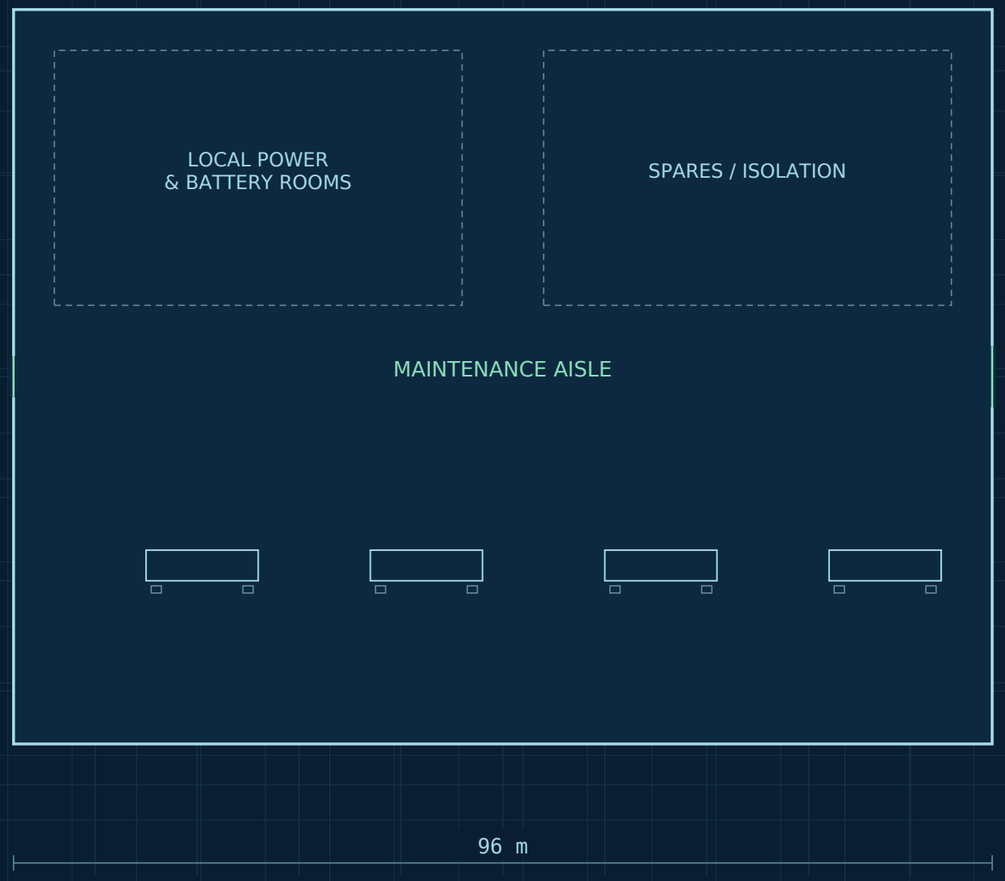

GRAPHIC SCALE


0 10 m

WORLD X = -136 + local x / Y = -84 + local y

LEVELS: -36 m

Separate zones can be isolated. A failure here cannot be written as an unexplained instant shutdown of all life support.

POSITION IN THE UNDERGROUND TOWN

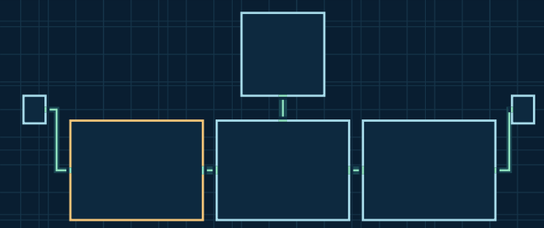

DAILY PURPOSE

Maintainable local power distribution, battery rooms, spare equipment and repair benches.

CONNECTIONS / WORLD XYZ

E / 6 m clear
(-88.0, -84, -36)


W / 4 m clear
(-184.0, -84, -36)

Linework fixes area allocation, key openings and functional zones. Individual rooms and fixtures can gain further registered detail within these bounds.

Water & Air Service Rooms

Area blueprint / world anchor (-30, -84, -36) m / inherited axes, new underground area

PLAN / NORTH UP / DIMENSIONS IN METRES

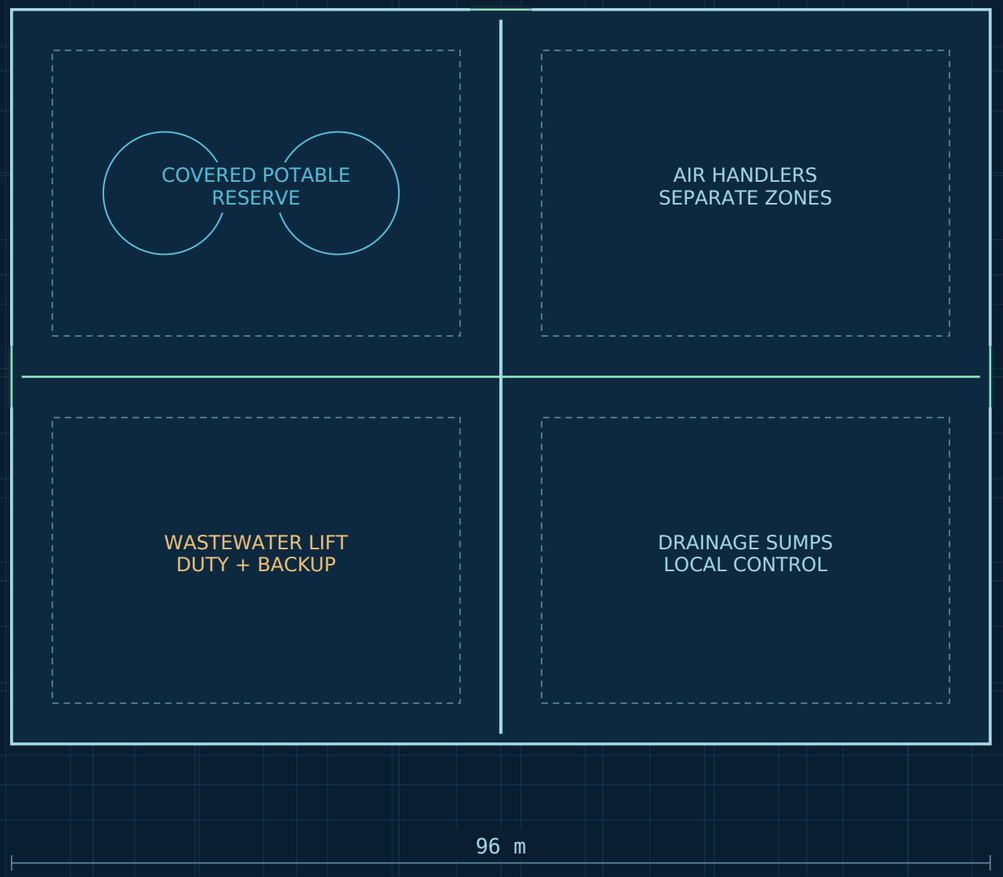

GRAPHIC SCALE


0 10 m

WORLD X = -30 + local x / Y = -84 + local y

LEVELS: -36 m

Wastewater must be pumped up to the existing -3 m service level; it cannot flow uphill by gravity. Independent duty/backup equipment and local controls.

POSITION IN THE UNDERGROUND TOWN

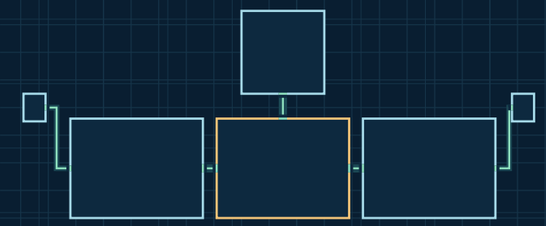

DAILY PURPOSE

Partitioned potable reserve, wastewater lift plant, drainage sumps and air-handling rooms.

CONNECTIONS / WORLD XYZ

W / 6 m clear
(-78.0, -84, -36)

E / 6 m clear
(18.0, -84, -36)


N / 6 m clear
(-30, -48.0, -36)

Linework fixes area allocation, key openings and functional zones. Individual rooms and fixtures can gain further registered detail within these bounds.

Deep Stores

Area blueprint / world anchor (76, -84, -36) m / inherited axes, new underground area

PLAN / NORTH UP / DIMENSIONS IN METRES

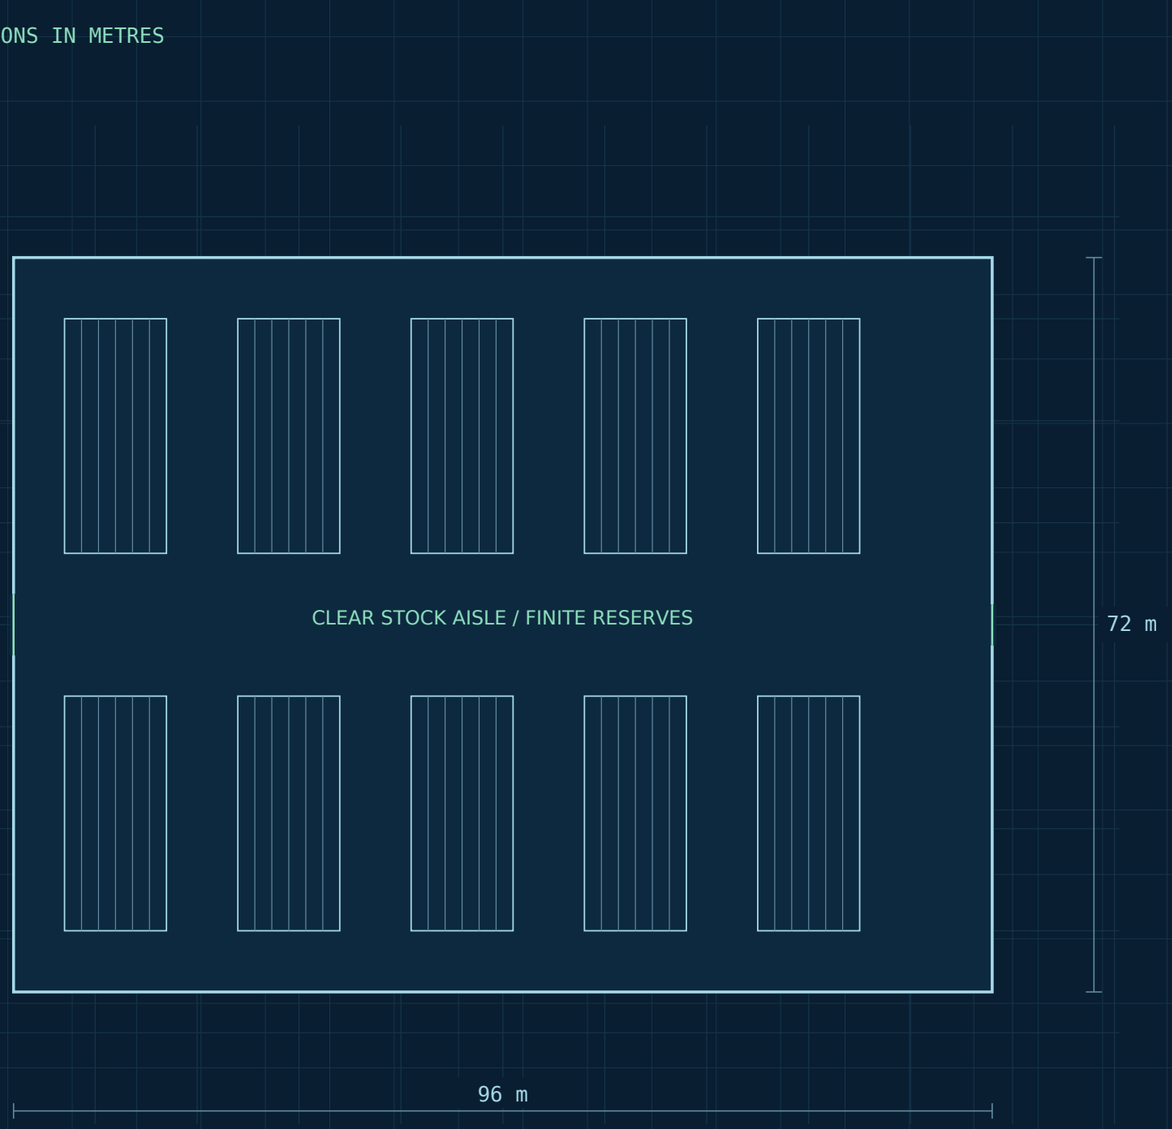

GRAPHIC SCALE


0 10 m

WORLD X = 76 + local x / Y = -84 + local y

LEVELS: -36 m

Stock quantities change in the event ledger. No infinite supplies or unearned emergency solution.

POSITION IN THE UNDERGROUND TOWN

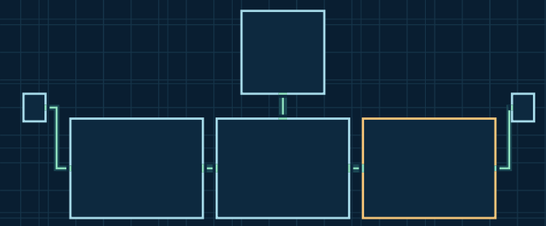

DAILY PURPOSE

Dry staples, household supplies, repair materials and documented community reserves.

CONNECTIONS / WORLD XYZ

W / 6 m clear
(28.0, -84, -36)


E / 4 m clear
(124.0, -84, -36)

Linework fixes area allocation, key openings and functional zones. Individual rooms and fixtures can gain further registered detail within these bounds.

West Stair & Refuge Core

Area blueprint / world anchor (-210, -40, -12) m / inherited axes, new underground area

PLAN / NORTH UP / DIMENSIONS IN METRES

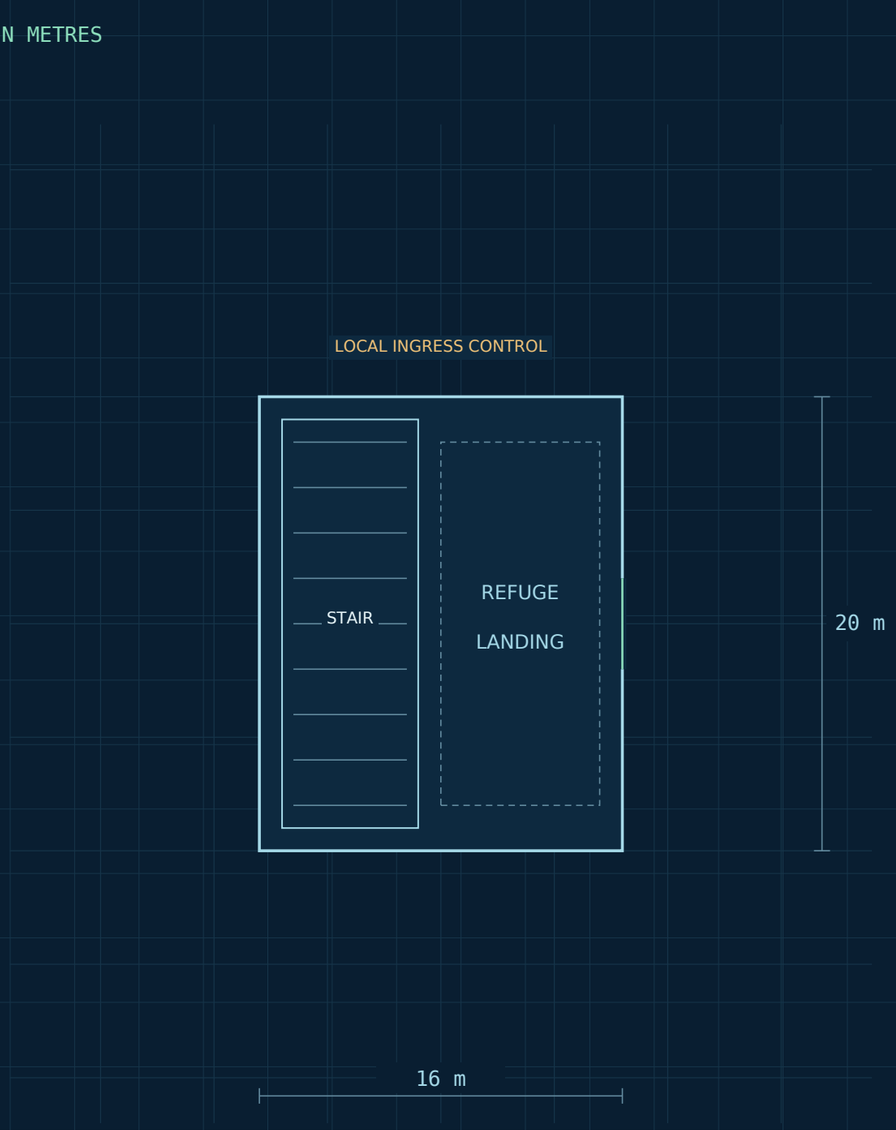

GRAPHIC SCALE


0 5 m

WORLD X = -210 + local x / Y = -40 + local y

LEVELS: -12 m, -24 m, -36 m

Outside entry is locally controlled. Occupants can leave from inside without network permission; surface conditions still determine whether evacuation is safe.

POSITION IN THE UNDERGROUND TOWN

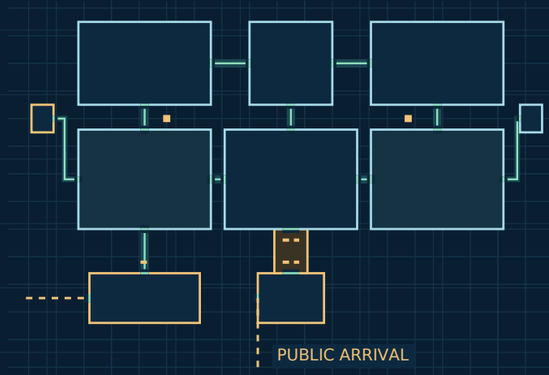

DAILY PURPOSE

An independent protected stair/refuge core links all three underground levels to the surface service walk at (-210,-40,0).

CONNECTIONS / WORLD XYZ

E / 4 m clear
(-202.0, -40, -12)

The same horizontal footprint and matching landings repeat at -12, -24 and -36 m. Stairs are independent of powered lifts.

Linework fixes area allocation, key openings and functional zones. Individual rooms and fixtures can gain further registered detail within these bounds.

East Stair & Refuge Core

Area blueprint / world anchor (144, -40, -12) m / inherited axes, new underground area

PLAN / NORTH UP / DIMENSIONS IN METRES



GRAPHIC SCALE


0 5 m

WORLD X = 144 + local x / Y = -40 + local y

LEVELS: -12 m, -24 m, -36 m

This is a distinct route from the west core. Include it in any surface-overrun state and keep staff able to operate it locally.

POSITION IN THE UNDERGROUND TOWN

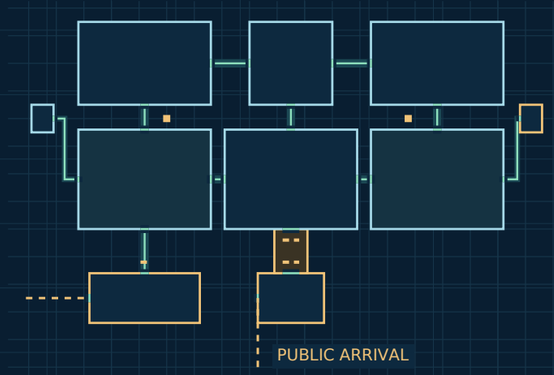

DAILY PURPOSE

A second separated protected stair/refuge core links all levels to the surface service walk at (144,-40,0).

CONNECTIONS / WORLD XYZ

W / 4 m clear
(136.0, -40, -12)

The same horizontal footprint and matching landings repeat at -12, -24 and -36 m. Stairs are independent of powered lifts.

Linework fixes area allocation, key openings and functional zones. Individual rooms and fixtures can gain further registered detail within these bounds.

World canon / a populated Burrow

Current edition v2.0.0 / owner-directed changes, daily life and story continuity

A FULL NEIGHBORHOOD WORLD

Plan for 2,400 residents: 800 in the outdoor district and 1,600 in four underground wards. The numbers are authored planning figures. Residents cross between both parts for work, learning, meals and leisure.

LIFE BELOW GROUND

Show doorsteps, household kitchens, children going to school, deliveries, laundry, quiet hours, workshops and neighbor-run shops. Warm light, varied door colors, planted communal pockets and readable street names distinguish districts.

WELCOMING ENTRANCES

Normal public access replaces the earlier closed-gate default. Visitors can reach public civic areas. Private homes and working service rooms retain ordinary boundaries; access never depends on a token, wallet or game rank.

DEFENSE AS A STATE

The underground town has a stronger independent boundary if the outdoor district is overrun. Gates, service thresholds and stair access are handled together. Local physical control, civilian refuge and breathable spaces remain essential.

EPISODE 1

Begin with ordinary life above and below. The underground is familiar and joyful before any clue. All four heroes appear through helpful actions. No pilot invasion, named villain or threatening bunker reveal.

SUBTLE CLUES

Retain the duplicate D17 receipt and Snow's unfamiliar physical trace. The final receipt can occur after a clearly established routine evening closing; daytime public access stays open.

WHAT REMAINS FIXED

Keep all 16 surface positions and footprints, three canal crossings, the watercourse, hero designs and approved voices. Snow has canine sounds only. No oversized Madger fang.

VERSION PRECEDENCE

This is v2.0.0 because the owner changed scope, population assumptions and access rules. Earlier editions stay archived. Their conflicting closed-gate and 400-resident statements are superseded.

REUSABLE FOR ALL CONTENT

Every future area receives a measured plan and registered connections. The drawing set guides stories, anime and game environments; it does not claim those releases are already rebuilt.